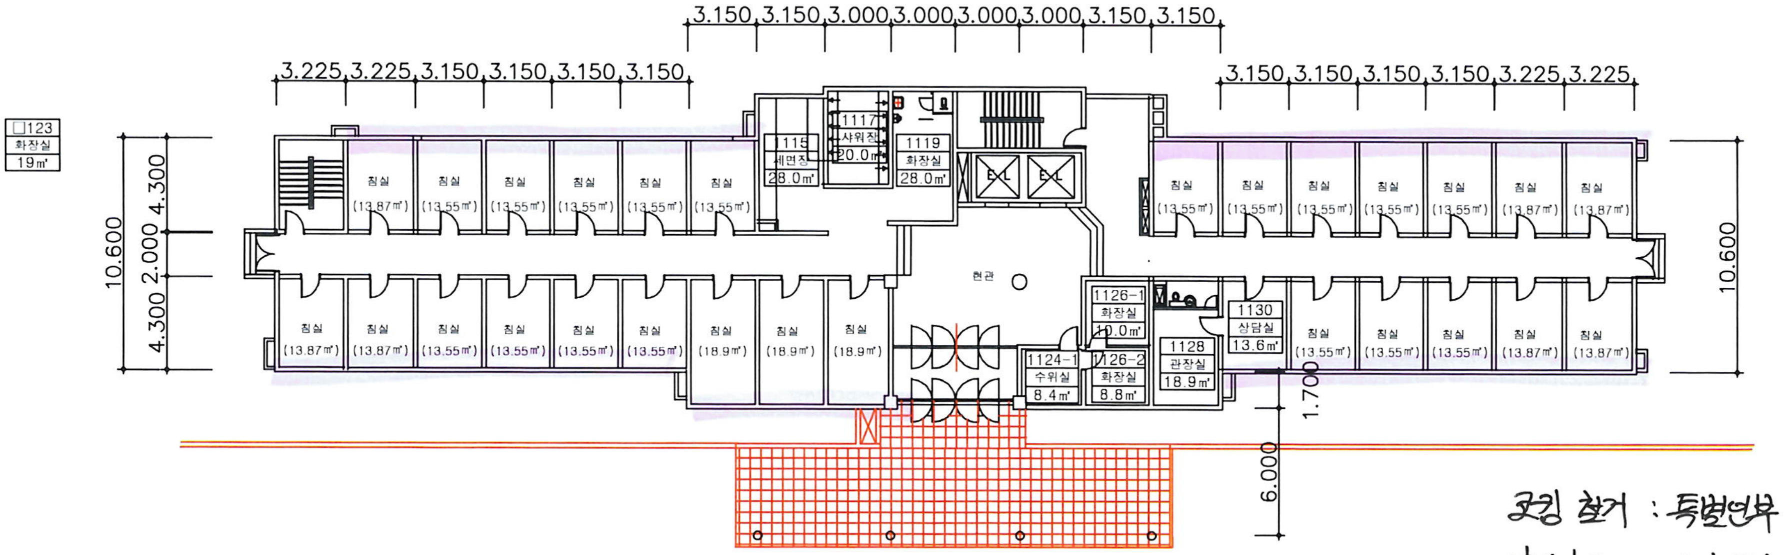
3.150 3.150 3.000 3.000 3.000 3.000 3.150 3.150
3.225 3.225 3.150 3.150 3.150 3.150
3.150 3.150 3.150 3.150 3.225 3.225
□123
화장실
19㎡
10.600
4.300
2.000
4.300
1.700
6.000
1115
세면장
28.0㎡
1117
샤워장
20.0㎡
1119
화장실
28.0㎡
E/L
E/L
현관
침실
(13.87㎡)
(13.55㎡)
(18.9㎡)
1126-1
화장실
10.0㎡
1124-1
수위실
8.4㎡
1126-2
화장실
8.8㎡
1128
관장실
18.9㎡
1130
상담실
13.6㎡

1층평면도

코킹 철거 : 특별인부 24인

장비사용 : 고소작업차 (5ton) : 48h

청소 및 폐기물 처리 : 보통인부 10인

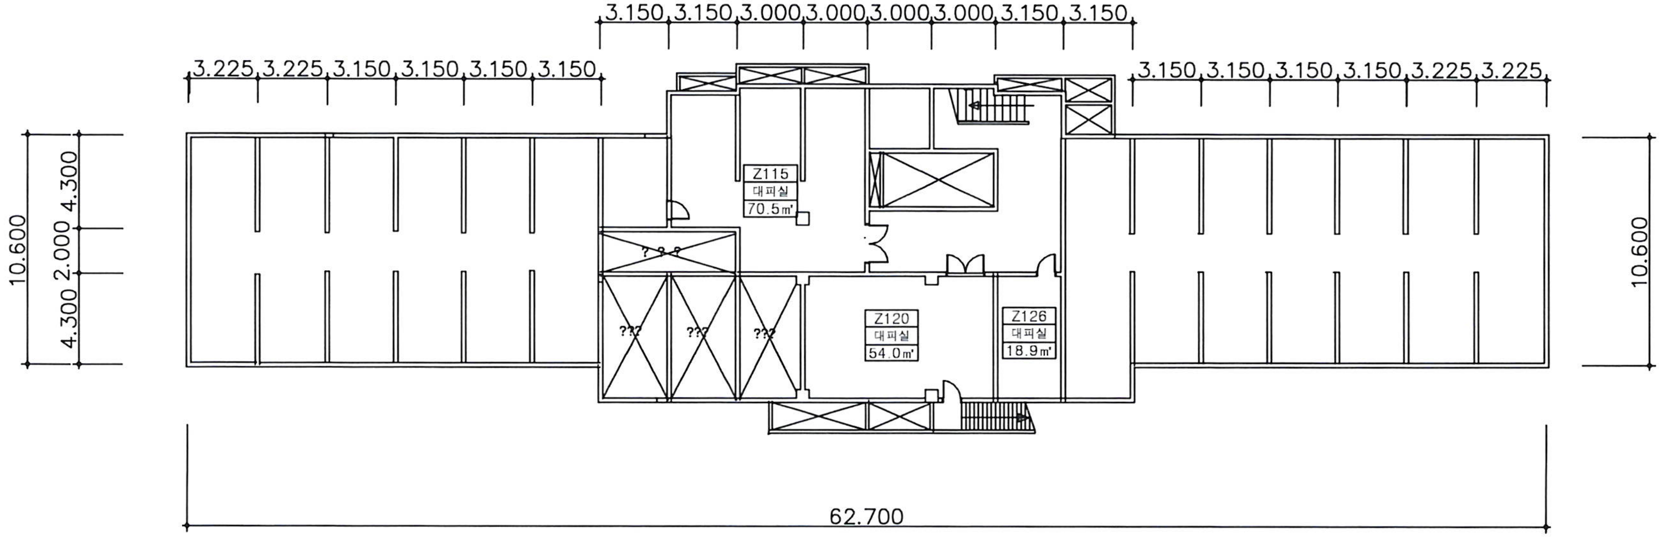
3.150 3.150 3.000 3.000 3.000 3.000 3.150 3.150
3.225 3.225 3.150 3.150 3.150 3.150
3.150 3.150 3.150 3.150 3.225 3.225
10.600
4.300
2.000
4.300
Z115
대피실
70.5㎡
Z120
대피실
54.0㎡
Z126
대피실
18.9㎡
???
62.700

지하층평면도

?????
WONKWANG UNIVERSIT

수정날짜 : 2016. 02. 18

건 물 명

생활관
(학림관)

複 ? ?

지하층평면도
1층평면도

축 척	도면번호
NONE	272

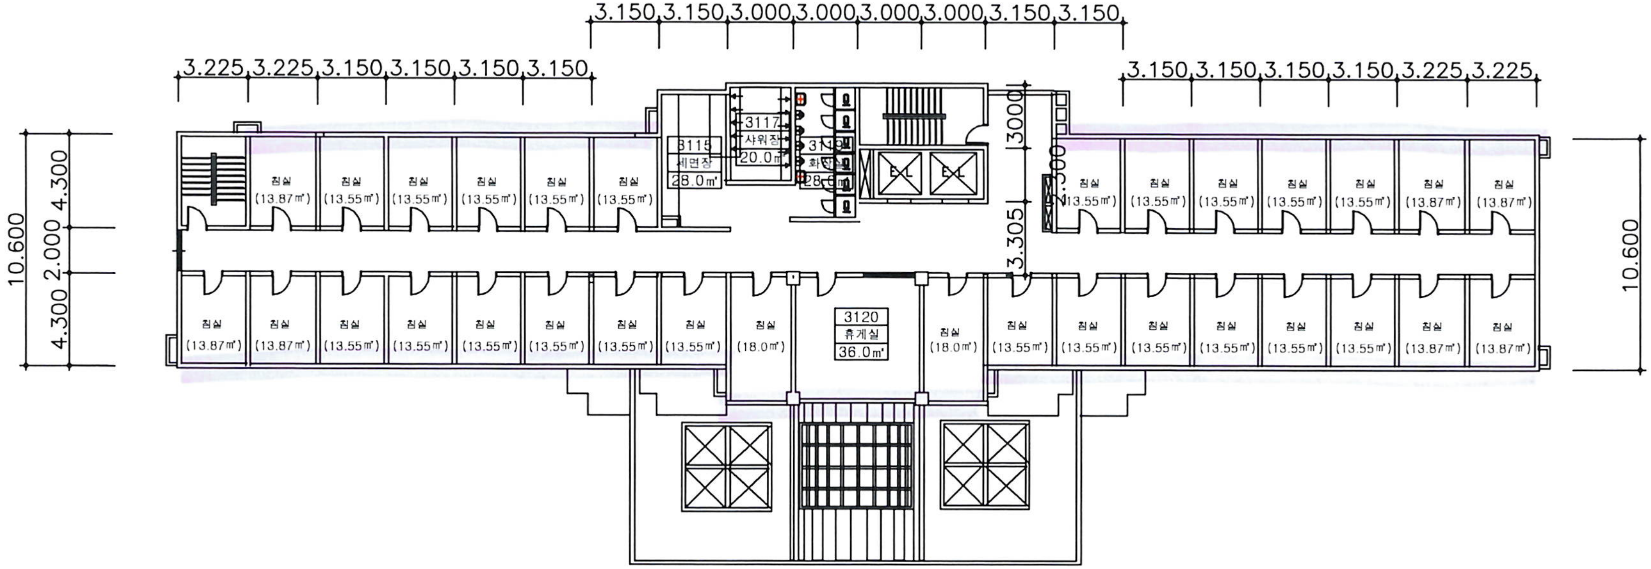
3.150 3.150 3.000 3.000 3.000 3.000 3.150 3.150
3.225 3.225 3.150 3.150 3.150 3.150
3.150 3.150 3.150 3.150 3.225 3.225
10.600
4.300
2.000
4.300
10.600
3000
2.500
3.305
3115
세면장
28.0㎡
3117
샤워장
20.0㎡
3119
화장실
28.0㎡
E.L
E.L
침실 (13.87㎡)
침실 (13.55㎡)
침실 (18.0㎡)
3120
휴게실
36.0㎡

3층평면도

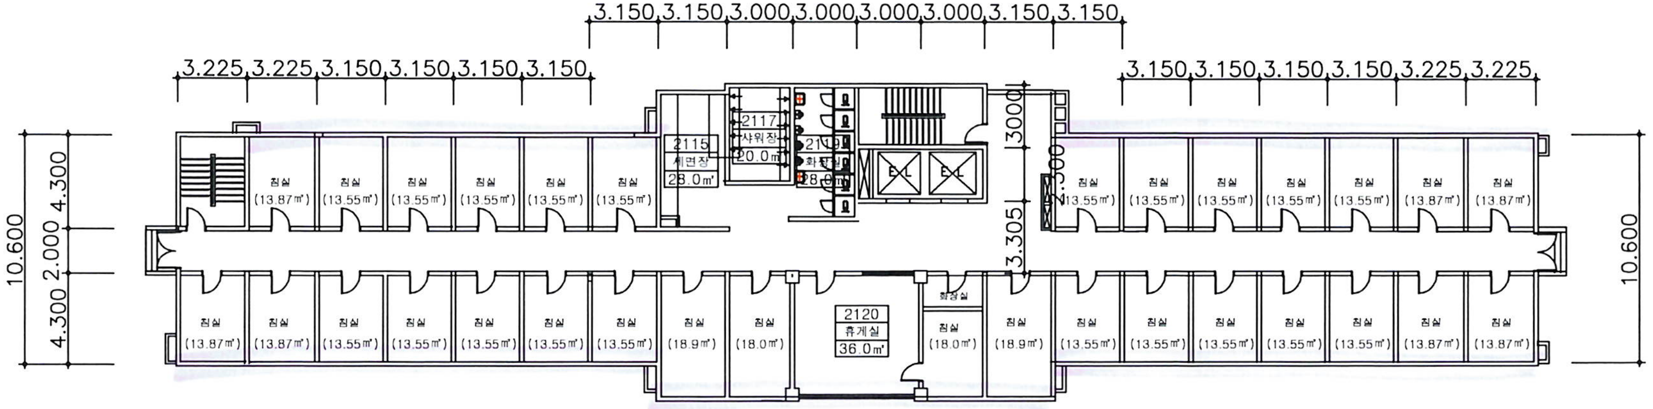
3.150 3.150 3.000 3.000 3.000 3.000 3.150 3.150
3.225 3.225 3.150 3.150 3.150 3.150
3.150 3.150 3.150 3.150 3.225 3.225
10.600
4.300
2.000
4.300
10.600
3000
2.500
3.305
2115
세면장
28.0㎡
2117
샤워장
20.0㎡
2119
화장실
28.0㎡
E.L
E.L
침실 (13.87㎡)
침실 (13.55㎡)
침실 (18.9㎡)
침실 (18.0㎡)
2120
휴게실
36.0㎡
화장실

2층평면도

?????
WONKWANG UNIVERSIT

수정날짜 : 2016. 02. 18

건 물 명

생활관
(학림관)

複 ? ?

2층평면도
3층평면도

축 척	도면번호
NONE	273

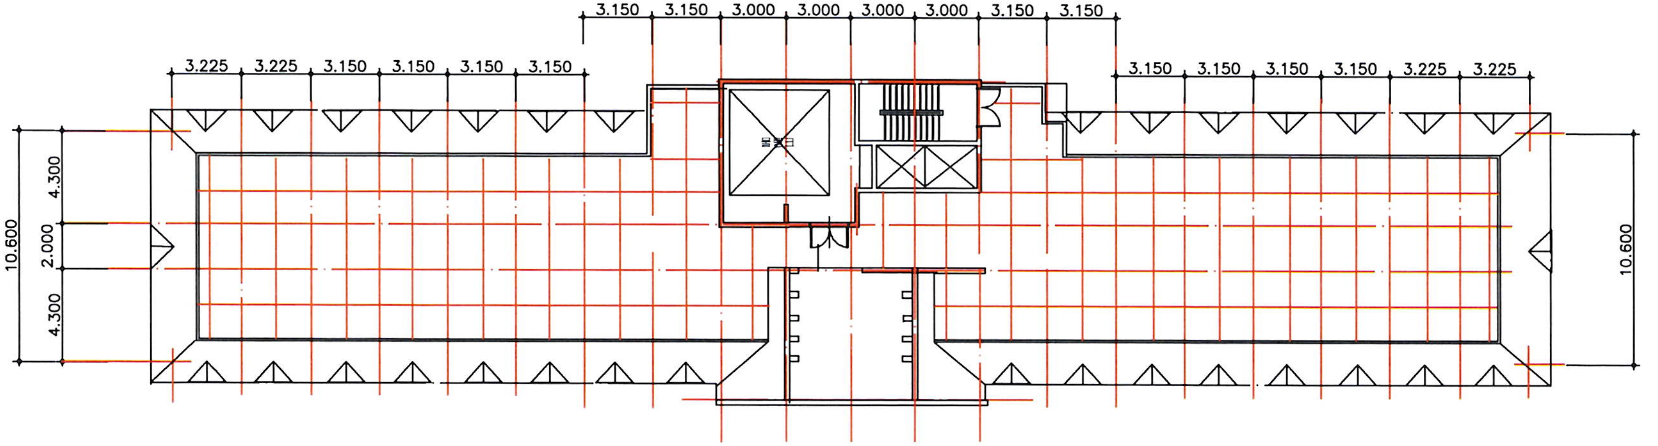
3.150
3.150
3.000
3.000
3.000
3.000
3.150
3.150
3.225
3.225
3.150
3.150
3.150
3.150
3.150
3.150
3.150
3.150
3.225
3.225
10.600
4.300
2.000
4.300
10.600
물탱크

옥탑1층평면도

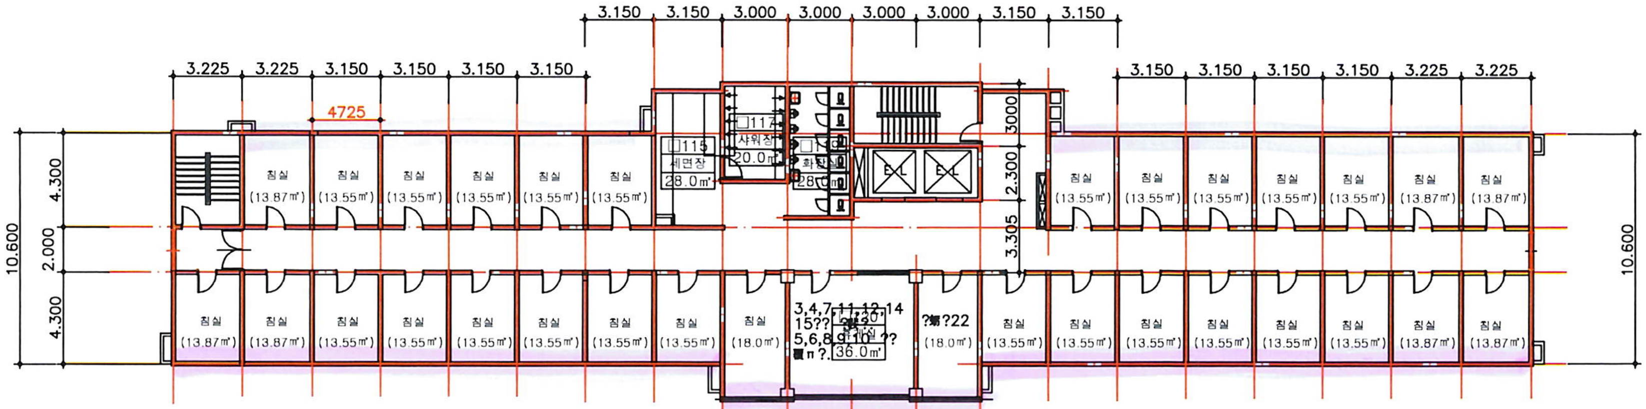
3.150
3.150
3.000
3.000
3.000
3.000
3.150
3.150
3.225
3.225
3.150
3.150
3.150
3.150
3.150
3.150
3.150
3.150
3.225
3.225
4725
10.600
4.300
2.000
4.300
3000
2.300
3.305
10.600
□115
세면장
28.0㎡
□117
샤워장
20.0㎡
□119
화장실
28.0㎡
E.L
E.L
침실
(13.87㎡)
침실
(13.55㎡)
침실
(18.0㎡)
3,4,7,11,12,14
15??
5,6,8,9,10 ??
휴게실
36.0㎡
?? ?22

4-15층평면도

?????
WONKWANG UNIVERSIT

수정날짜 : 2016. 02. 18

건 물 명

생활관
(학림관)

複 ? ?

4~15층 평면도
옥탑 1층 평면도

축 척	도면번호
NONE	274