

소방기호 범례

	유도등	1
B1F 1F	계단통로유도등	1

대형 벽부형	1
소형 계단통로유도등	1

숭산기념관 천정 리모델링공사


주식회사 다 울

1 : 150 (A3) 2026. 05 ? ? ?

숭산기념관 지하층 전기시설 교체 평면도 E - 0 9

다진 건축사무소

지하층 공사구분계획도

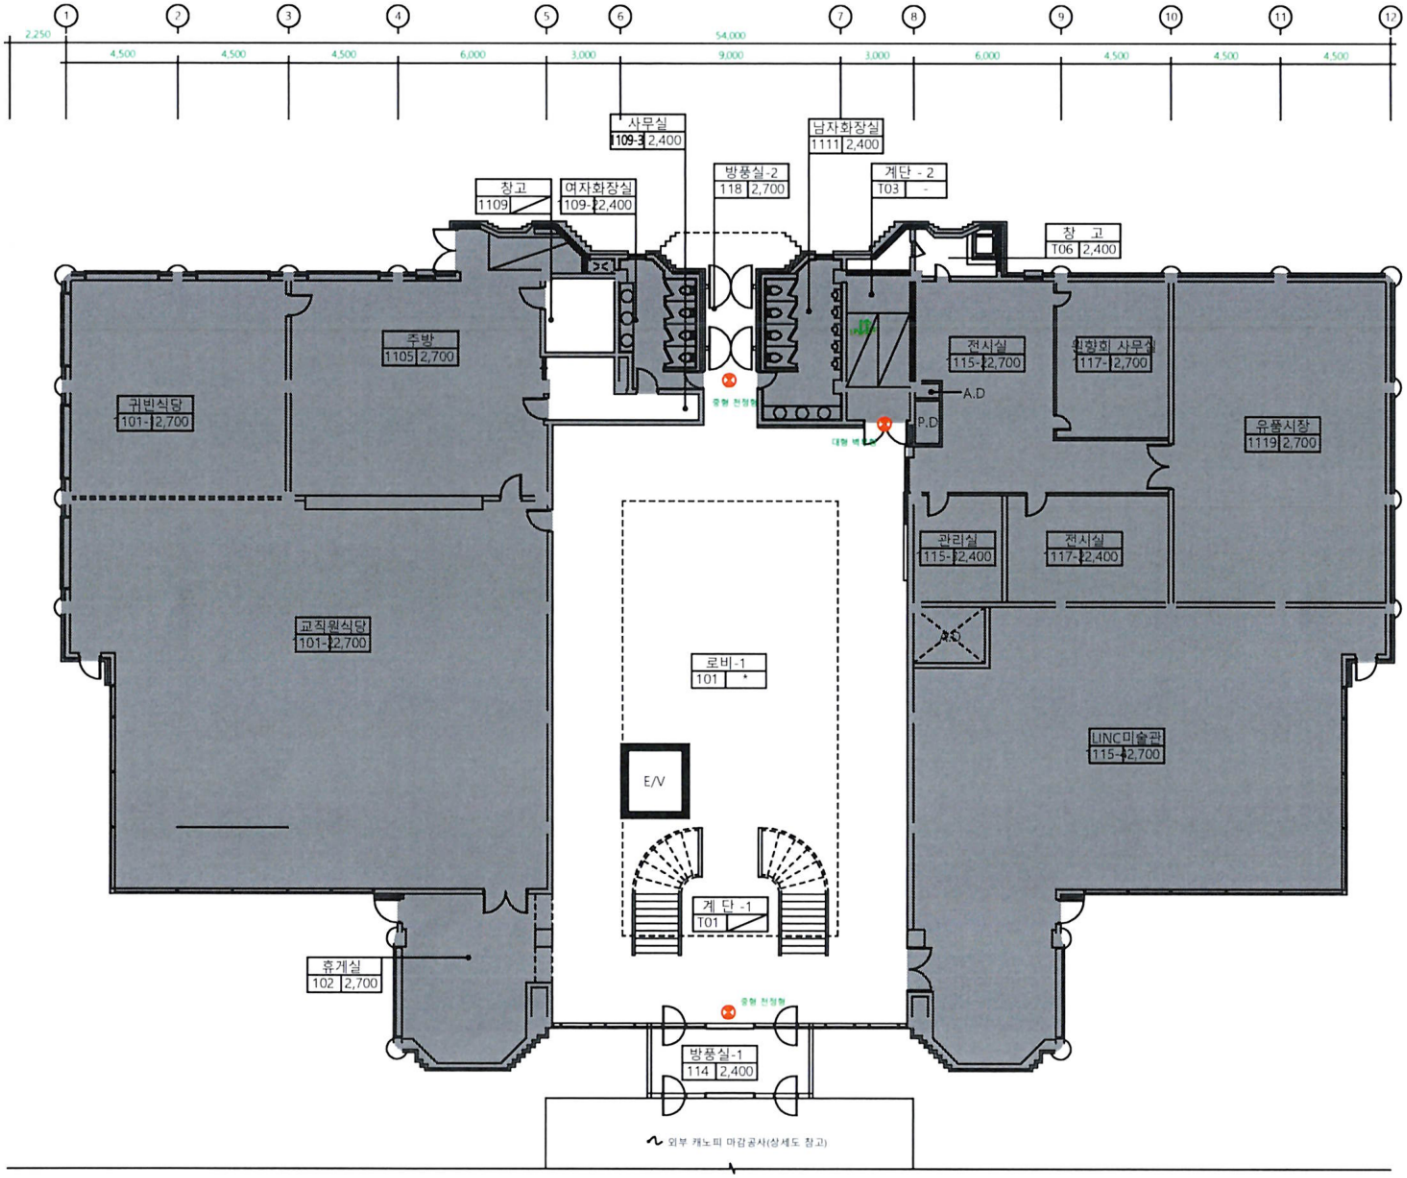

지상1층 공사구분계획도

SCALE : 1/200

소방기호 범례


유도등	3
계단통로유도등	1
대형 벽부형	1
중형 천정형	2
소형 계단통로유도등	1

도면명: 지상1층 공사구분계획도

축척: A1 : 1/100, A3 : 1/200

PJ CODE	작성	검토	승인
0000			

도면번호: A-002

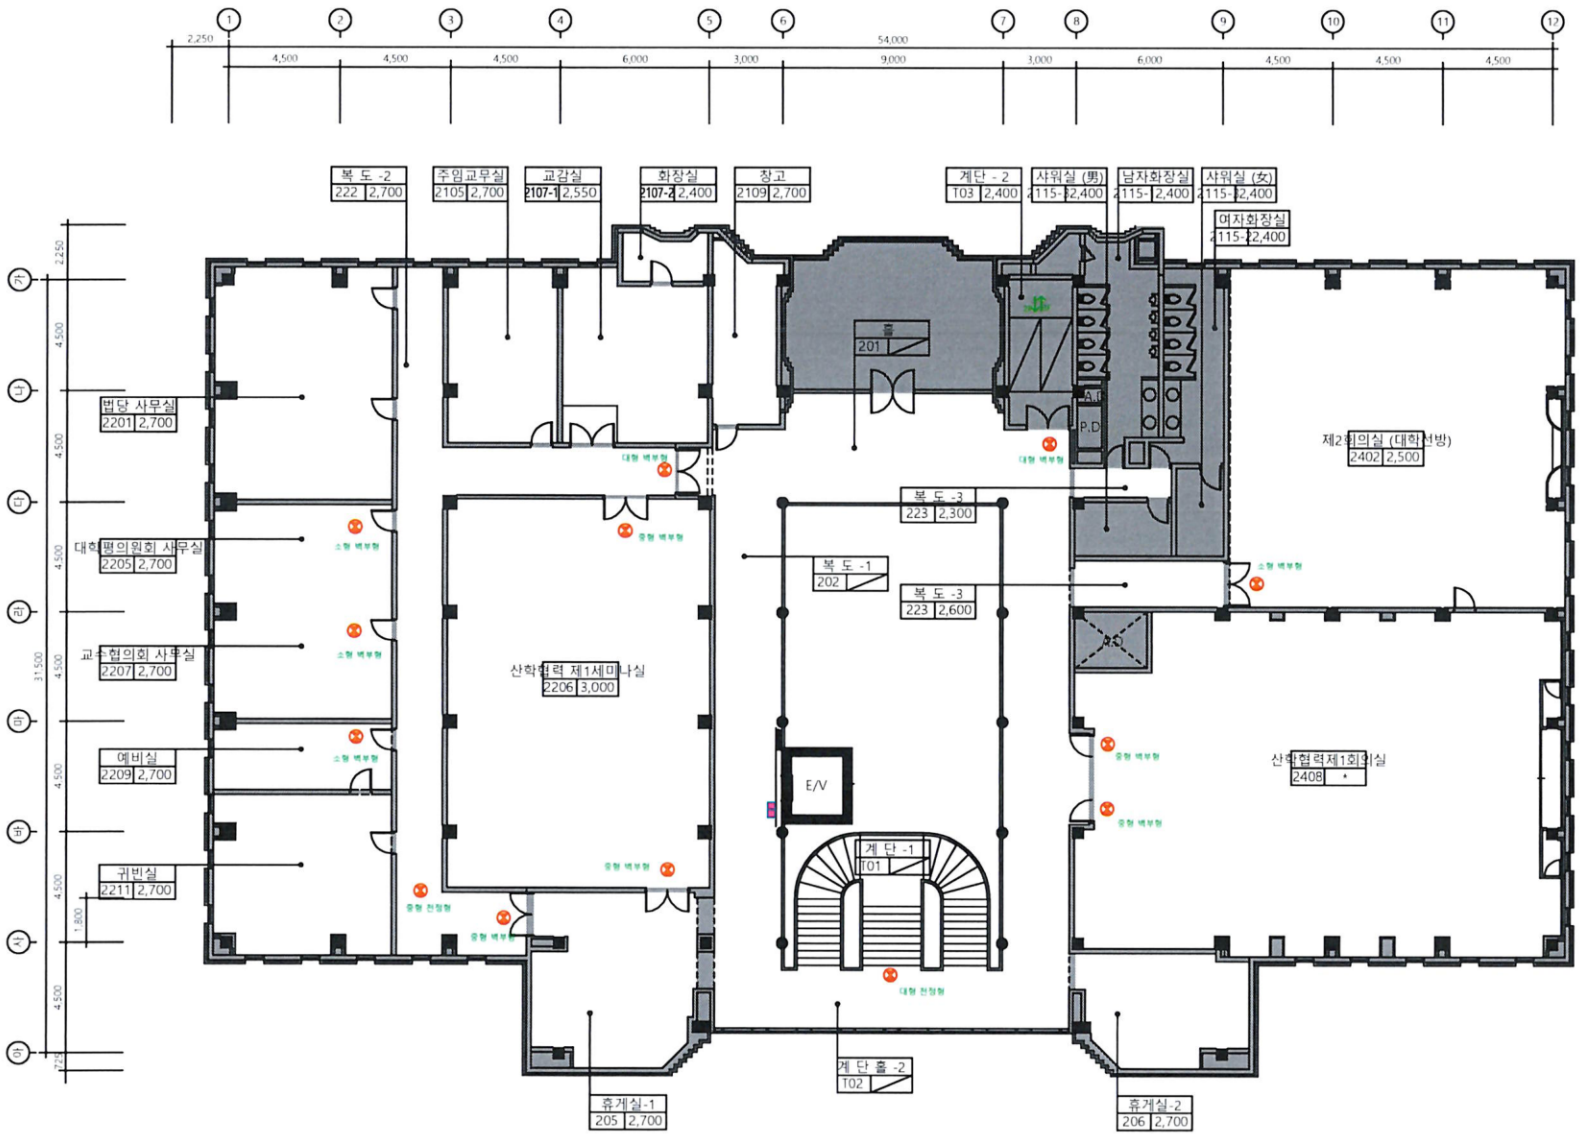

지상2층 공사구분계획도

SCALE : 1/200

소방기호 범례


	유도등	13
	계단통로유도등	1
	대형 벽부형	2
	대형 천정형	1
	중형 천정형	1
	중형 벽부형	5
	소형 벽부형	4
	소형 계단통로유도등	1

도면명: 지상2층 공사구분계획도

축척: A1 : 1/100, A3 : 1/200

PJ CODE	작성	검토	승인
0000			

도면번호: A-003

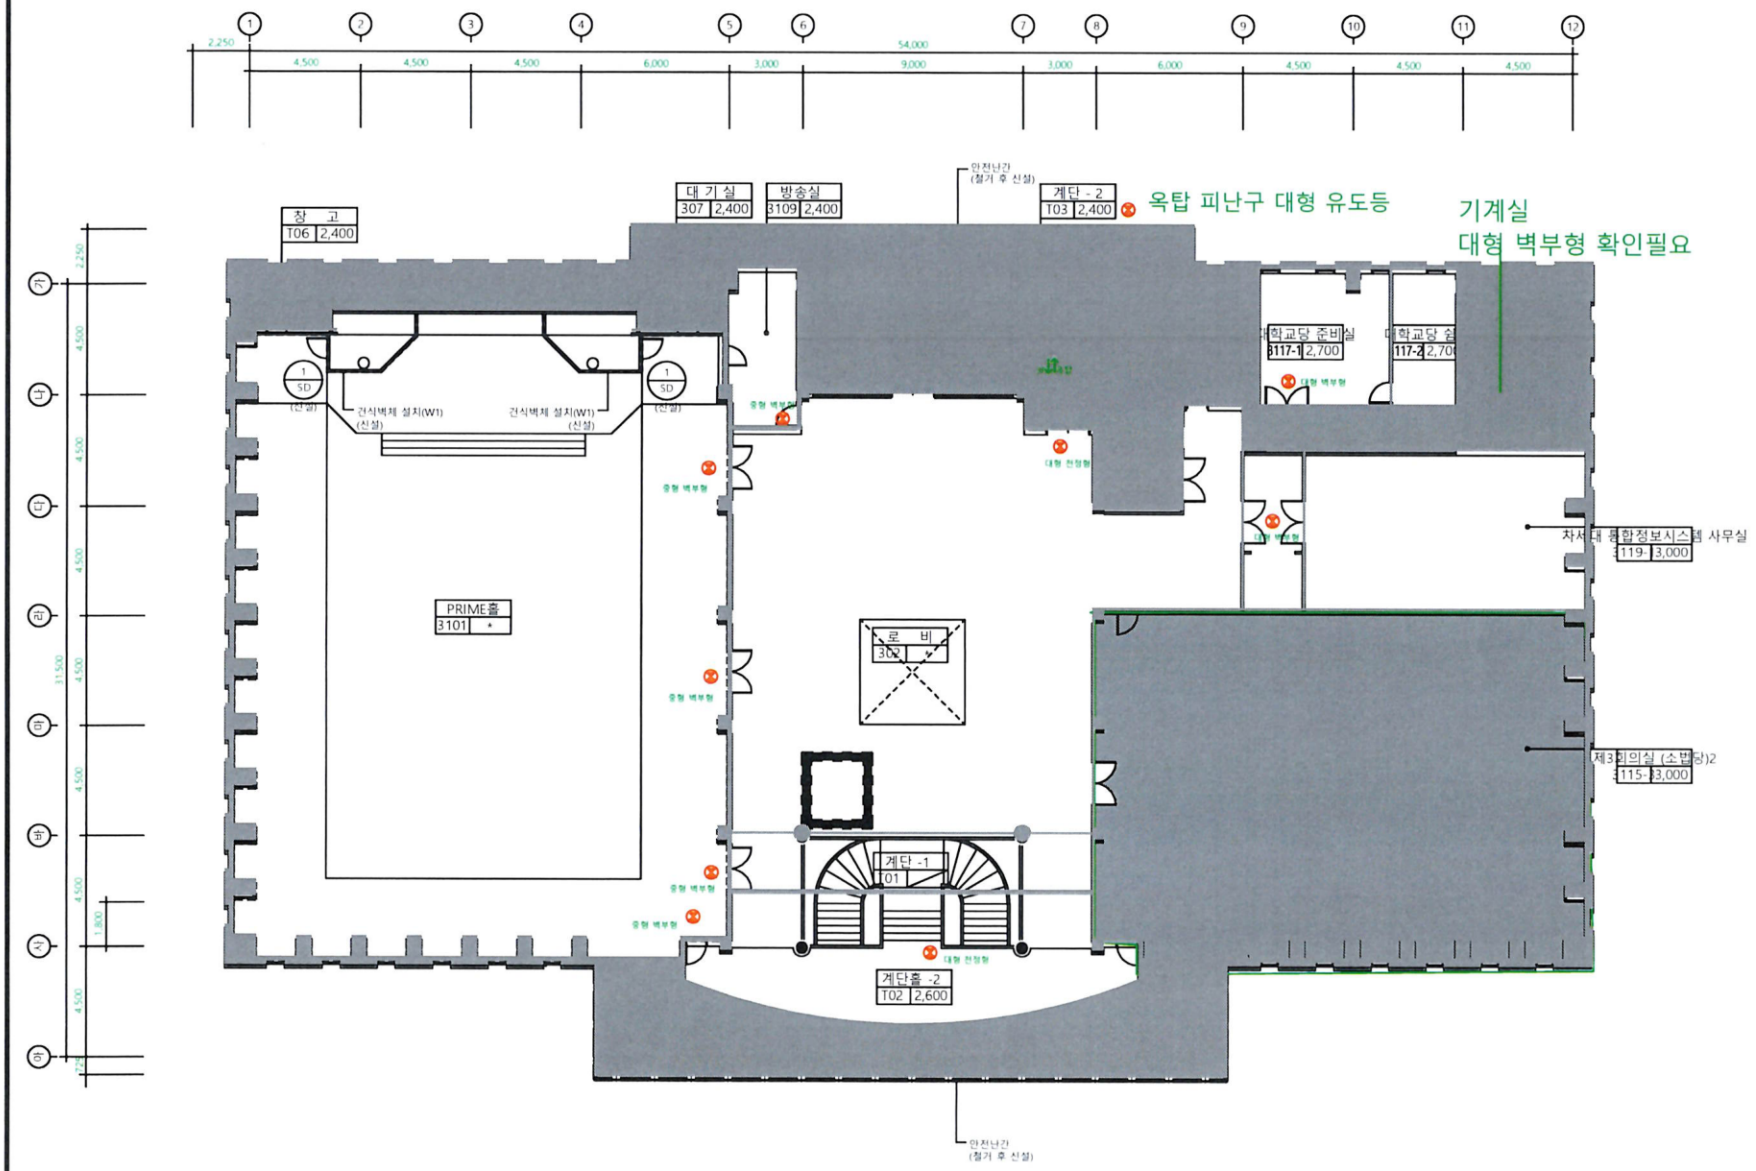

지상3층 공사구분계획도

SCALE : 1/200

소방기호 범례

유도등	10
계단통로유도등	1
대형 벽부형 (옥탑 포함)	3
대형 천장형	2
중형 벽부형	5
소형 계단통로유도등	1

도면명	지상3층 공사구분계획도
축척	A1 : 1/100 A3 : 1/200
PJ CODE	0000
작성	
검토	
승인	
도면번호	A-004