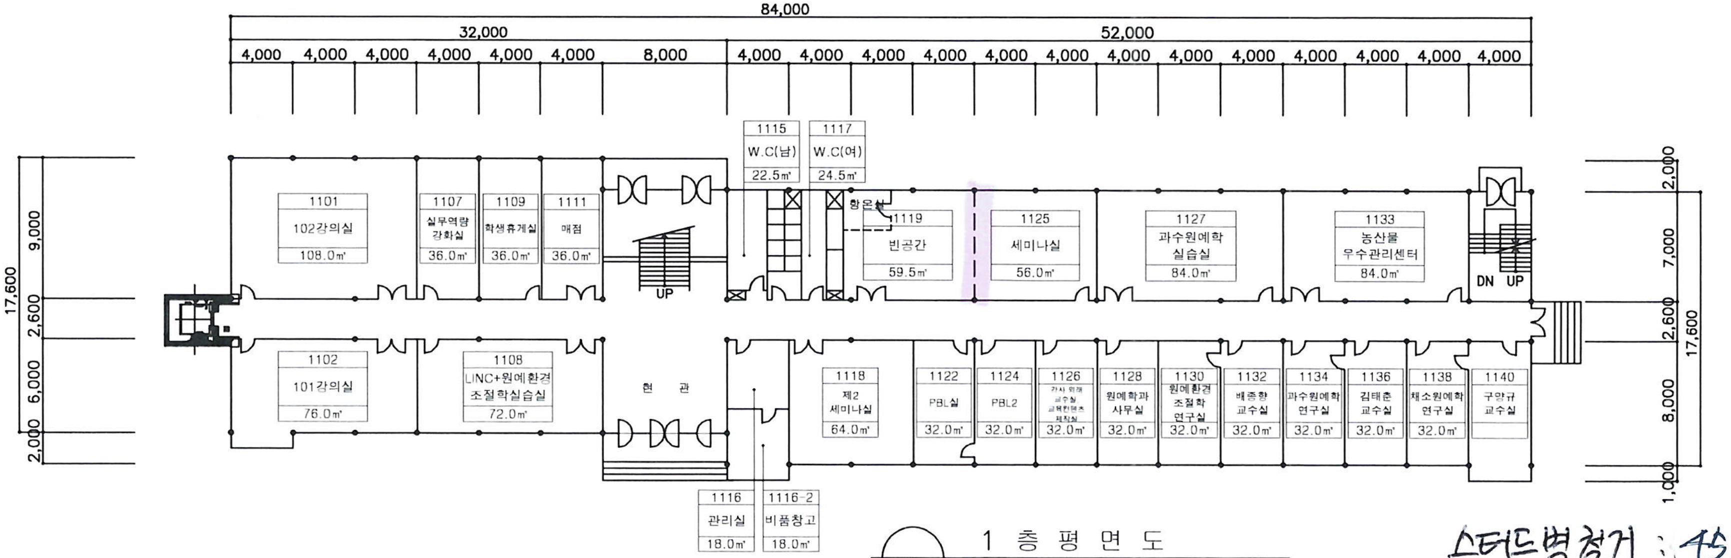
84,000
32,000
52,000
4,000
8,000
17,600
9,000
2,600
6,000
2,000
7,000
8,000
1,000
1101
102강의실
108.0㎡
1107
실무역량 강화실
36.0㎡
1109
학생휴게실
36.0㎡
1111
매점
36.0㎡
UP
1115
W.C(남)
22.5㎡
1117
W.C(여)
24.5㎡
항온실
1119
빈공간
59.5㎡
1125
세미나실
56.0㎡
1127
과수원예학 실습실
84.0㎡
1133
농산물 우수관리센터
84.0㎡
DN
UP
1102
101강의실
76.0㎡
1108
LINC+원예환경 조절학실습실
72.0㎡
현 관
1116
관리실
18.0㎡
1116-2
비품창고
18.0㎡
1118
제2 세미나실
64.0㎡
1122
PBL실
32.0㎡
1124
PBL2
32.0㎡
1126
강사 외래 교수실 교육컨텐츠 제작실
32.0㎡
1128
원예학과 사무실
32.0㎡
1130
원예환경 조절학 연구실
32.0㎡
1132
배종향 교수실
32.0㎡
1134
과수원예학 연구실
32.0㎡
1136
김태춘 교수실
32.0㎡
1138
채소원예학 연구실
32.0㎡
1140
구양규 교수실

1 층 평 면 도

스터드벽철거 : 45.5m²

석고보드 해체 : 182m²

조적 해체 : 4.2m³

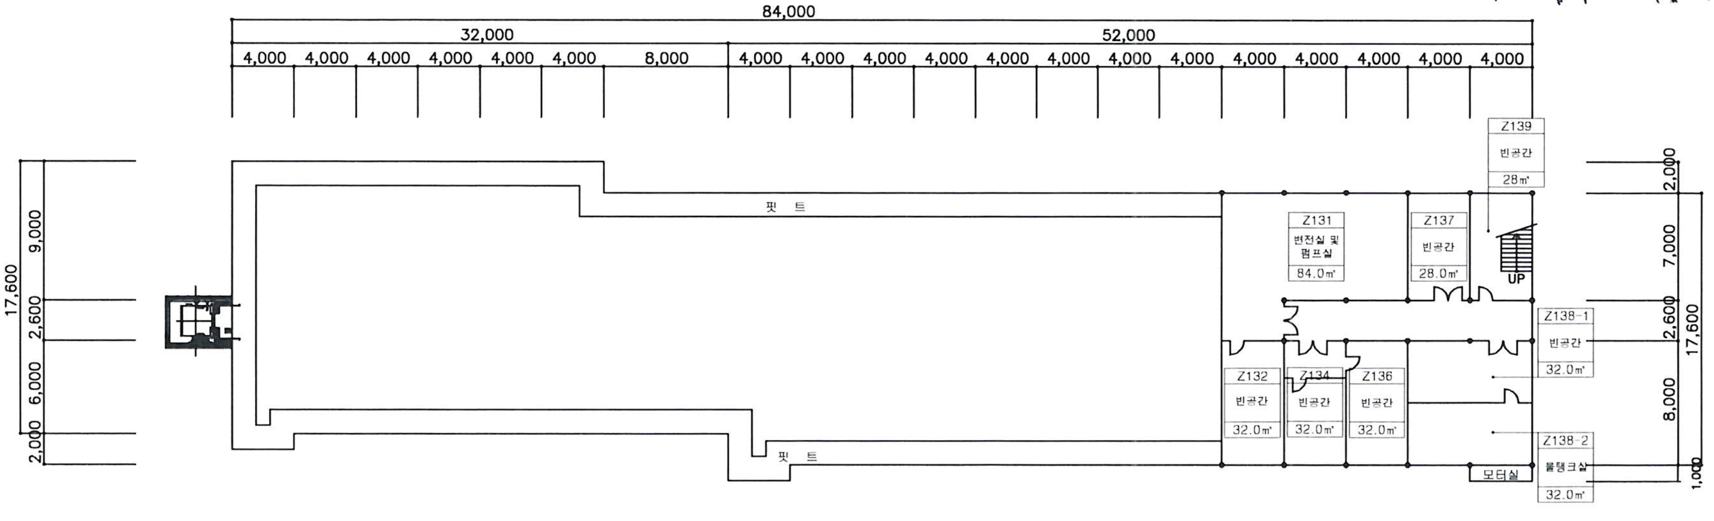
84,000
32,000
52,000
4,000
8,000
17,600
9,000
2,600
6,000
2,000
7,000
8,000
1,000
핏 트
핏 트
Z131
변전실 및 펌프실
84.0㎡
Z137
빈공간
28.0㎡
Z139
빈공간
28㎡
UP
Z138-1
빈공간
32.0㎡
Z132
빈공간
32.0㎡
Z134
빈공간
32.0㎡
Z136
빈공간
32.0㎡
모터실
Z138-2
물탱크실
32.0㎡

지 하 층 평 면 도 S : 1/150

?????
WONKWANG UNIVERSIT

※ NOTE

실번호	0000-0
실명	0 0 0
면적	000㎡

수정날짜 : 2023. 09. 01

공 사 명

생명자원과학관

도 면 명

지하층 평면도
1층 평면도

축 척	도 면 번 호
NONE	88

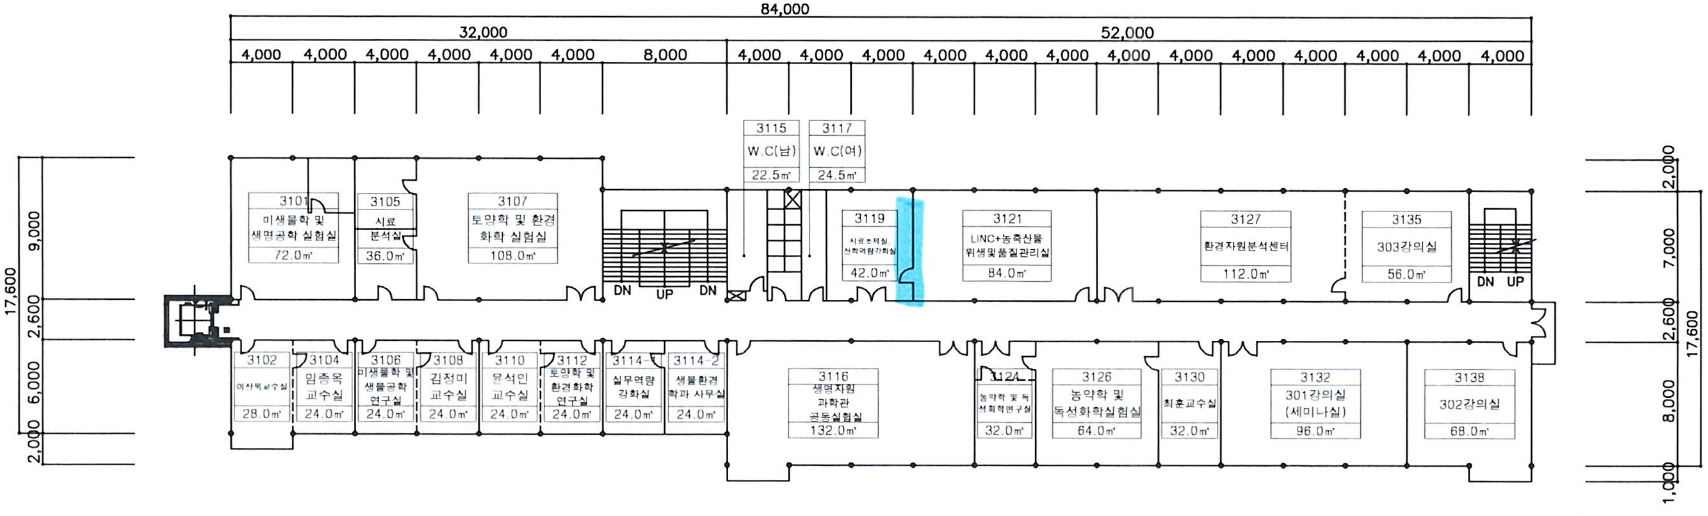
84,000
32,000
52,000
4,000
8,000
17,600
9,000
2,600
6,000
2,000
7,000
8,000
1,000
3101 미생물학 및 생명공학 실험실 72.0㎡
3105 시료 분석실 36.0㎡
3107 토양학 및 환경 화학 실험실 108.0㎡
3115 W.C(남) 22.5㎡
3117 W.C(여) 24.5㎡
3119 시료조제실, 산학역량강화실 42.0㎡
3121 LINC+농축산물 위생및품질관리실 84.0㎡
3127 환경자원분석센터 112.0㎡
3135 303강의실 56.0㎡
DN
UP
3102 이삼목교수실 28.0㎡
3104 임종옥 교수실 24.0㎡
3106 미생물학 및 생물공학 연구실 24.0㎡
3108 김정미 교수실 24.0㎡
3110 윤석인 교수실 24.0㎡
3112 토양학 및 환경화학 연구실 24.0㎡
3114-1 실무역량 강화실 24.0㎡
3114-2 생물환경 학과 사무실 24.0㎡
3116 생명자원 과학관 공동실험실 132.0㎡
3124 농약학 및 독성화학연구실 32.0㎡
3126 농약학 및 독성화학실험실 64.0㎡
3130 최훈교수실 32.0㎡
3132 301강의실 (세미나실) 96.0㎡
3138 302강의실 68.0㎡

3 층 평 면 도

스터드 설치: 70m

단열재 : 24.5m²

석고보드 : 98m²

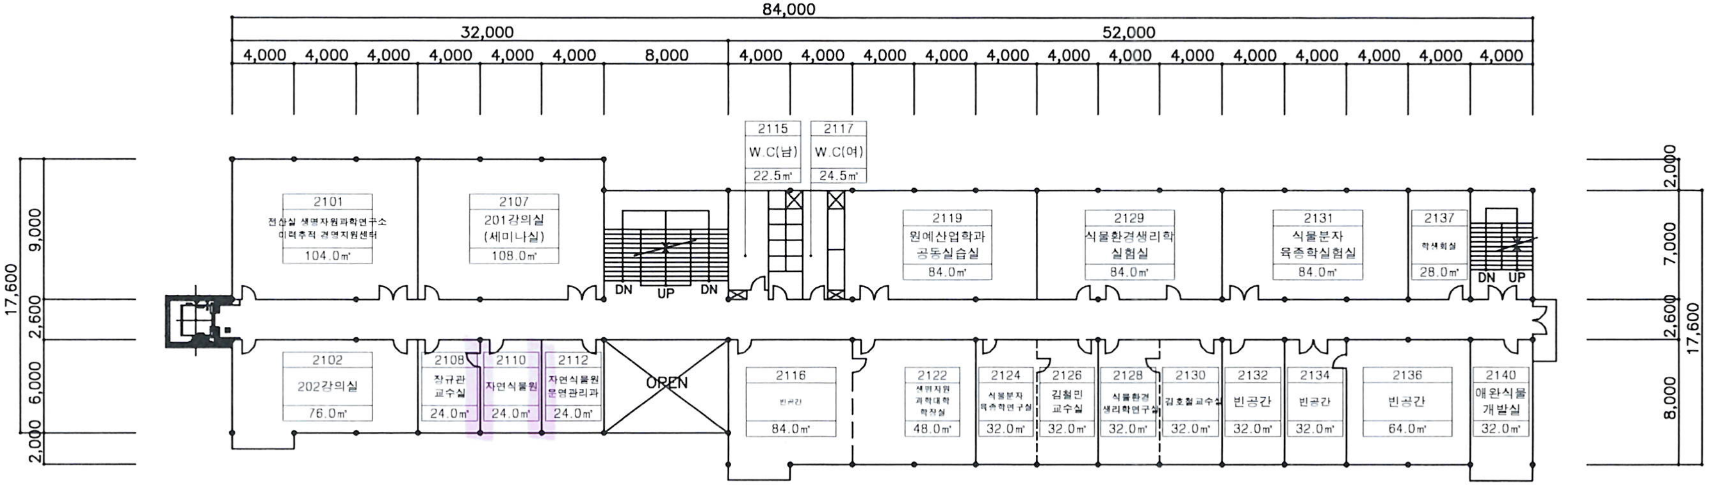
84,000
32,000
52,000
4,000
8,000
17,600
9,000
2,600
6,000
2,000
7,000
8,000
2101 전산실 생명자원과학연구소 이력추적 경영지원센터 104.0㎡
2107 201강의실 (세미나실) 108.0㎡
2115 W.C(남) 22.5㎡
2117 W.C(여) 24.5㎡
2119 원예산업학과 공동실습실 84.0㎡
2129 식물환경생리학 실험실 84.0㎡
2131 식물분자 육종학실험실 84.0㎡
2137 학생회실 28.0㎡
DN
UP
2102 202강의실 76.0㎡
2108 장규관 교수실 24.0㎡
2110 자연식물원 24.0㎡
2112 자연식물원 운영관리과 24.0㎡
OPEN
2116 빈공간 84.0㎡
2122 생명자원 과학대학 학장실 48.0㎡
2124 식물분자 육종학연구실 32.0㎡
2126 김철민 교수실 32.0㎡
2128 식물환경 생리학연구실 32.0㎡
2130 김호철교수실 32.0㎡
2132 빈공간 32.0㎡
2134 빈공간 32.0㎡
2136 빈공간 64.0㎡
2140 애완식물 개발실 32.0㎡

2 층 평 면 도

WONKWANG UNIVERSIT

※ NOTE

실번호	0000-0
실명	0 0 0
면적	000㎡

수정날짜 : 2023. 09. 01

건 물 명

생명자원과학관

도 면 명

2층 평면도
3층 평면도

축 척	도 면 번 호
NONE	89