


NOTE

1. 본 공사는 주 변전실내 기존 노후 케이블헤드 및 옥고압기기를 철거,교체하는 공사임.
2. 공사내용 : 주 변전실 내 케이블헤드 교체 및 지지애자 교체
3. 기타 공사중 발생하는 사항은 발주처 및 감리원과 협의하여 시공할 것.


주변전실 수변전설비 단선결선도

~ 3차전압 17.650 kV
2023.08 현재

- 케이블헤드(CH) 교체 및 CT 교체 (확대 결선도 참조)

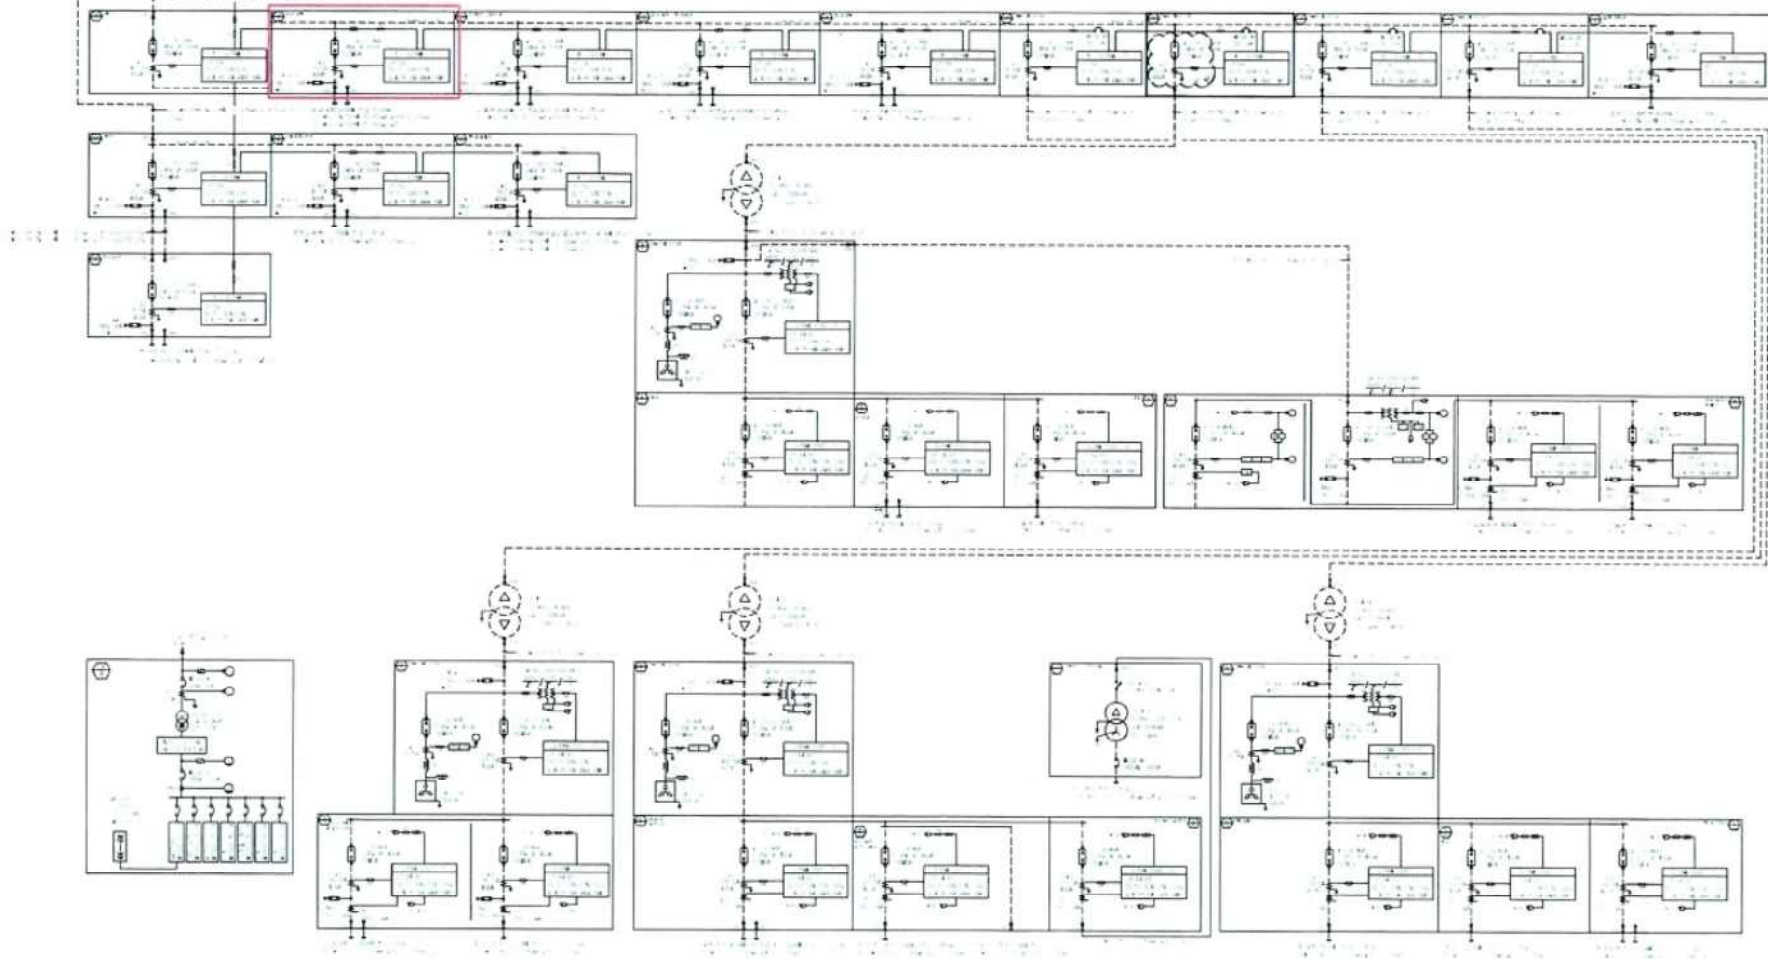

주	식	명	식	명	원	비	의	의	사	제	성	일	년	월	일	도	면	장	도	면	장	
가인과학부 석사학위논문발표회			 원광대학교			대한엔지니어링			E.N.S.TAD			2023.08			과장			주변전실 수변전설비 단선결선도 (전체)			Page 13	

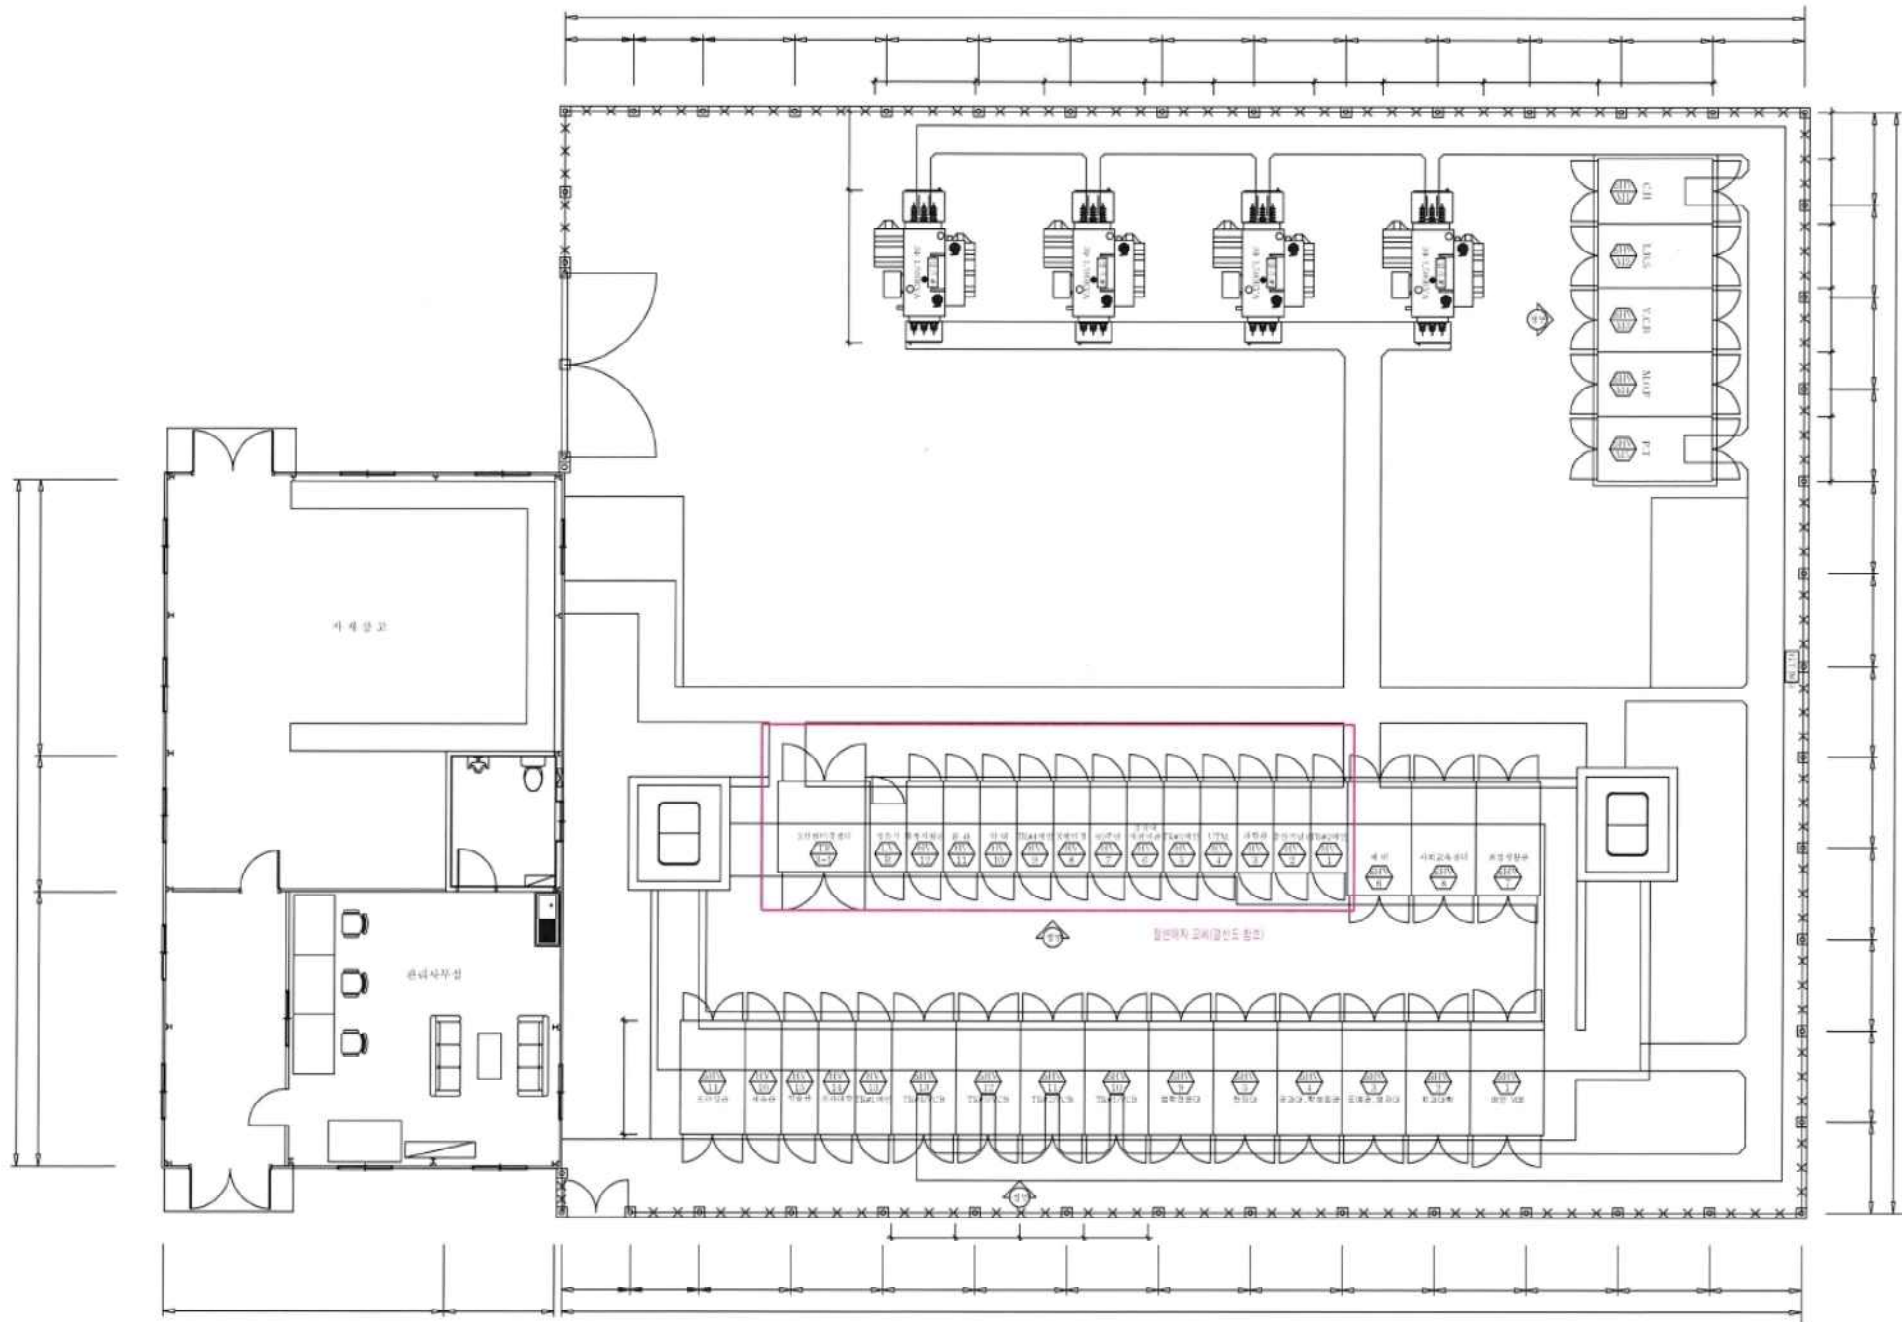

주변전실 확대 평면도(부분교체)

공 사 명	시 행 성	유 역 회 사	축 리	설 계 자	도 면 명	도 면 번호
자연과학관 및 약학관 면전실 교체공사	원 광 대 학 교	대한엔지니어링	1 : 120 (A3)	2025. 08	주변전실 확대 평면도(부분교체)	E - 15