

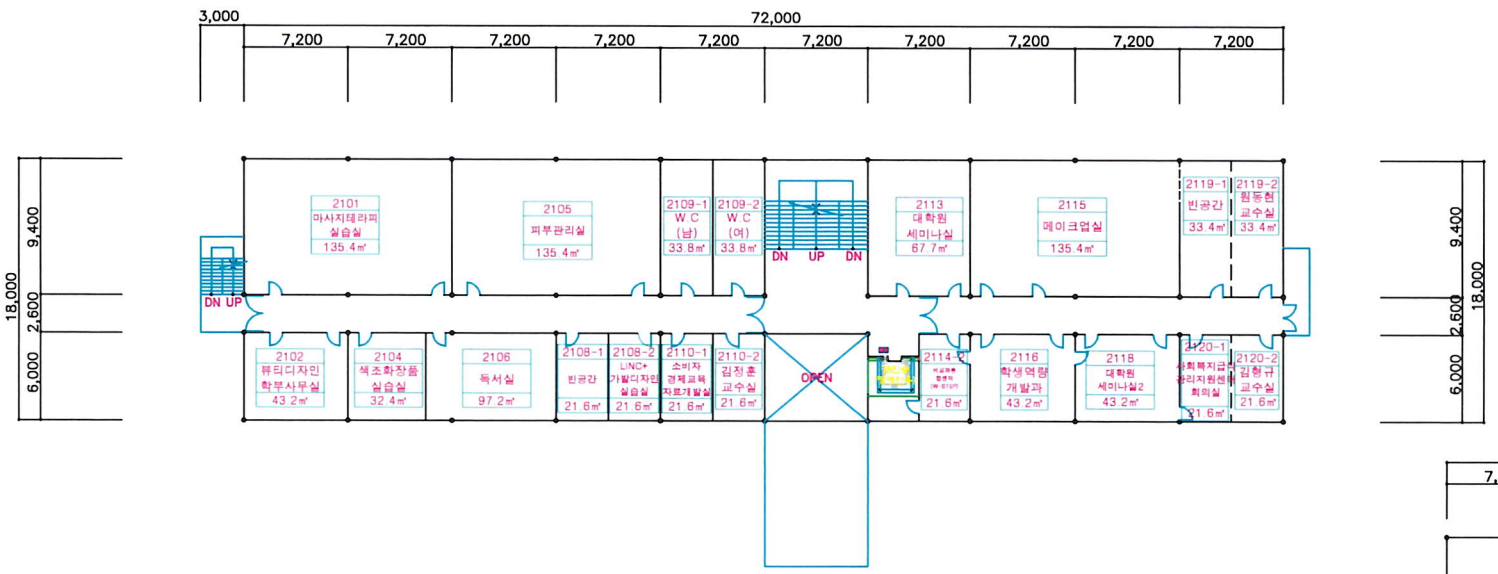


2 층 평 면 도

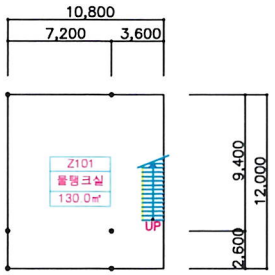

지 하 층 평 면 도

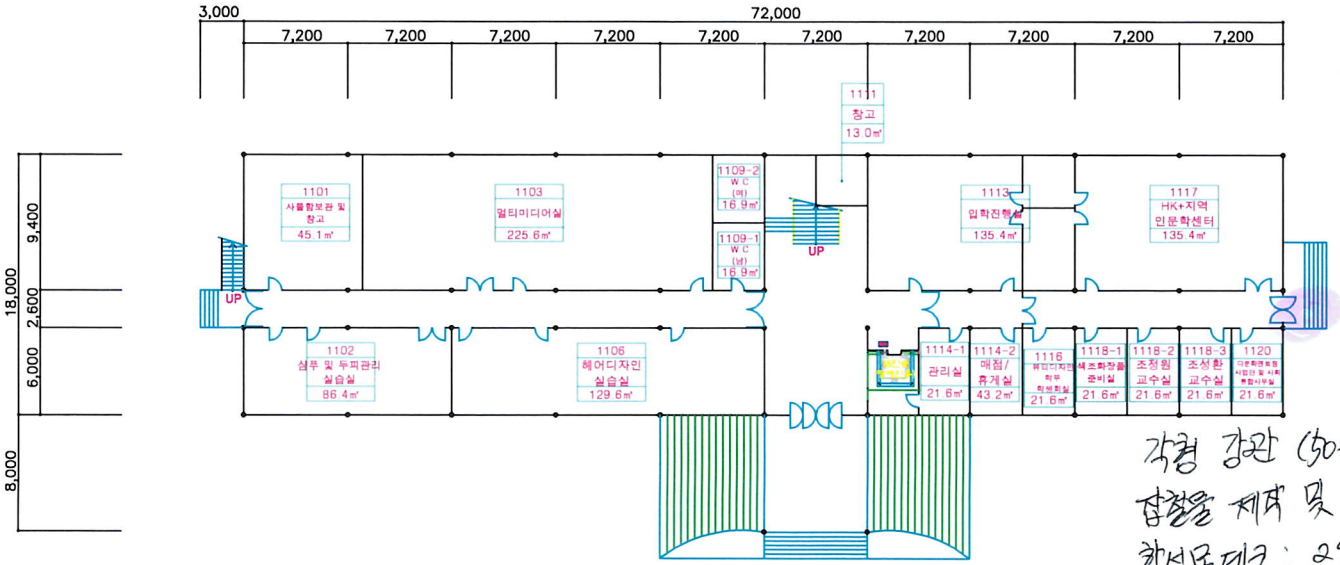

1 층 평 면 도

각형 강관 (50×50×2.2T) : 126m
잡철을 제작 및 설치 : 0.56ton
합성목데크 : 29.8㎡
AL 난간대 : 14m

※ NOTE

실번호	0000-0
실명	0 0 0
면적	000㎡

수정날짜 : 2024. 04. 02

건 물 명

생 활 대

도 면 명

지하층평면도
1층평면도
2층평면도

축 척	도면번호
NONE	95