

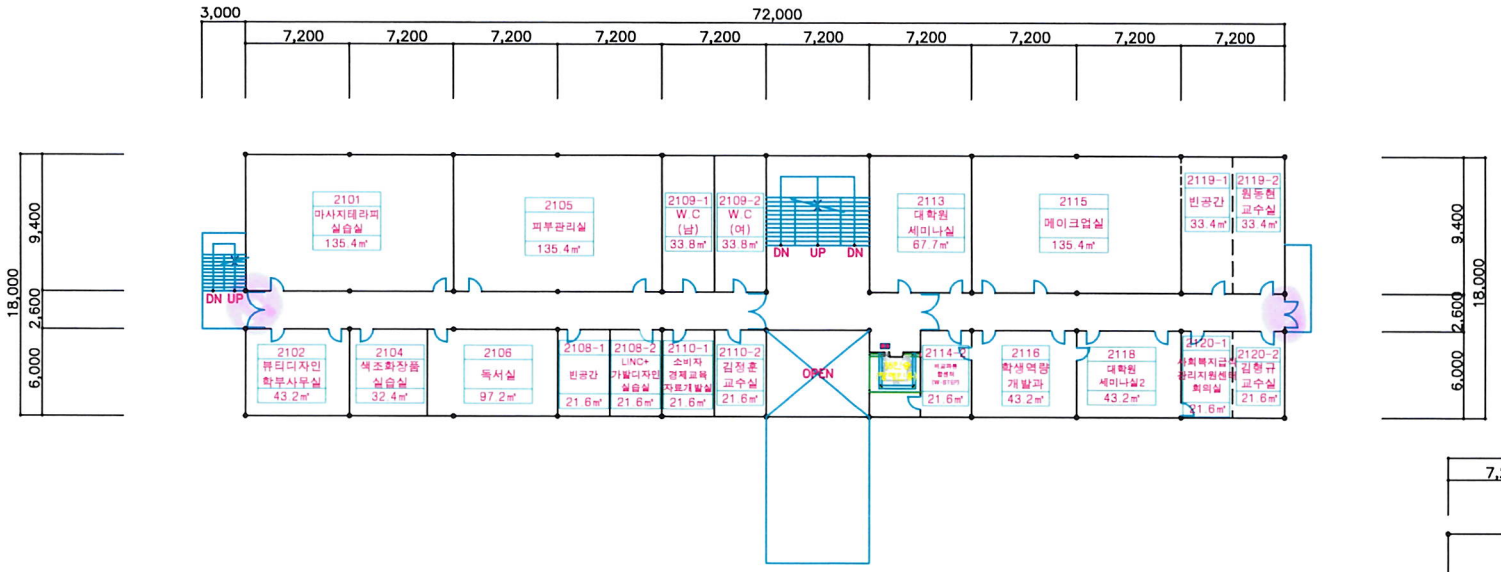


2 층 평 면 도

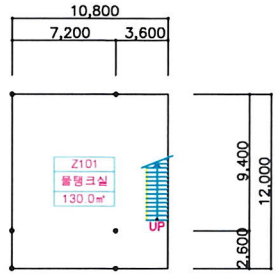

지 하 층 평 면 도

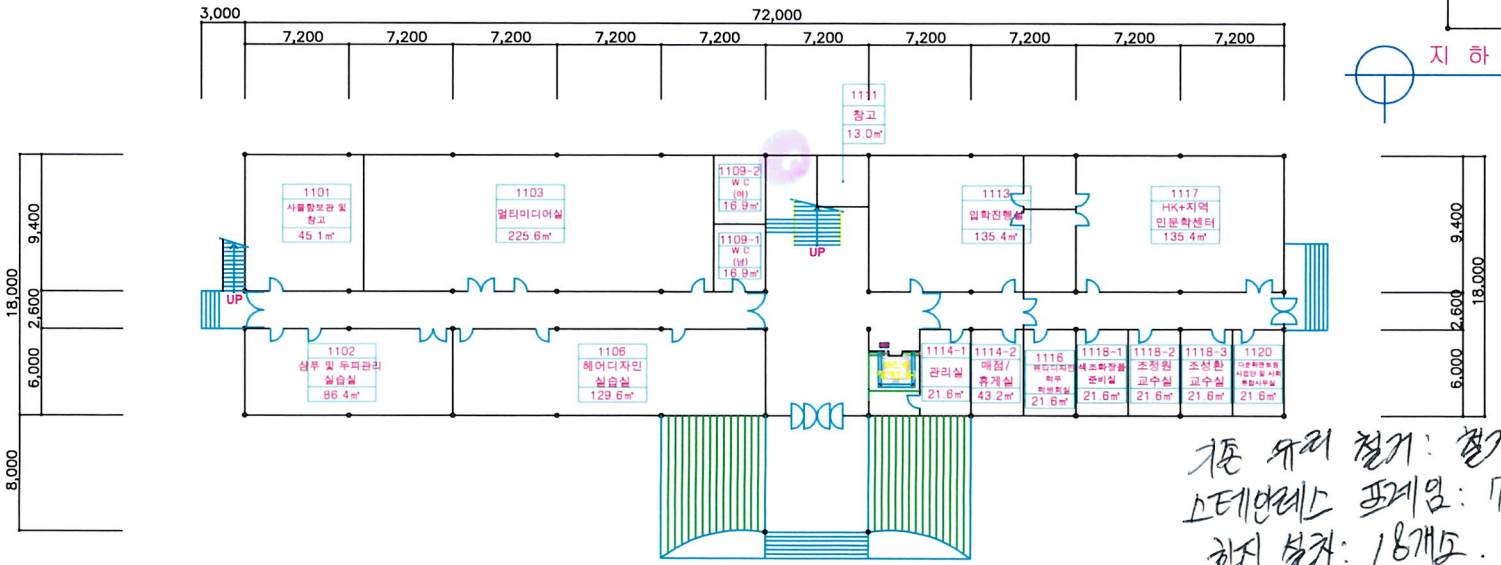

1 층 평 면 도

정비사용 : 12h

기존 유리 철거 : 철거용 4인
스테인레스 프레임 : 179.8m
한지 설치 : 18개소.
유리개루기 : 8T - 14.72m²
12T - 4.96m²
코킹 : 159.6m

※ NOTE

실번호	0000-0
실명	0 0 0
면적	000㎡

수정날짜 : 2024. 04. 02


건 물 명

생 활 대


도 면 명

지하층평면도
1층평면도
2층평면도

축 척	도면번호
NONE	95

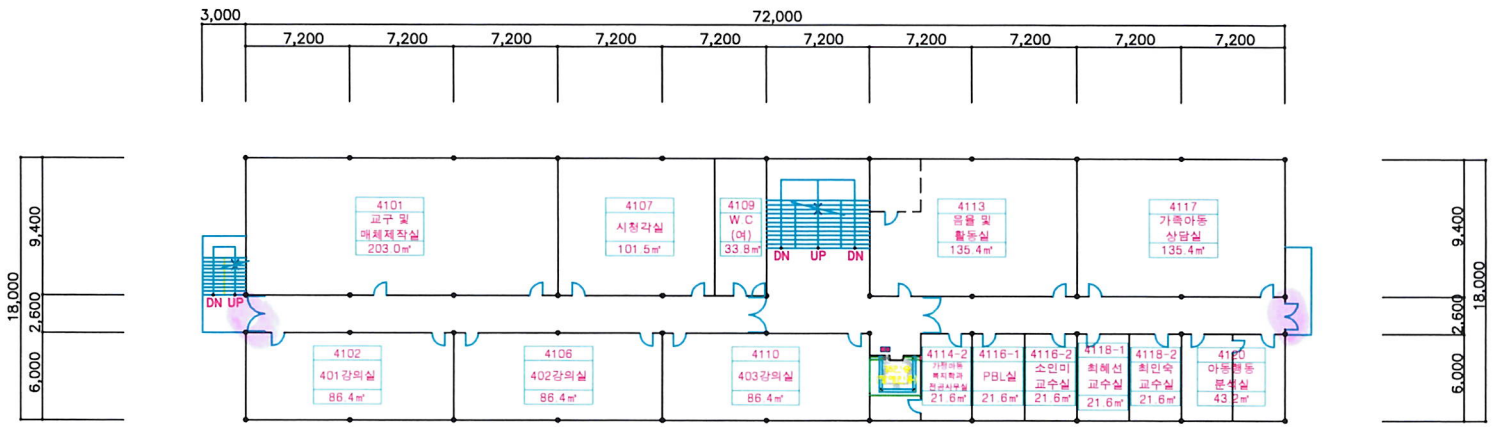

4층평면도

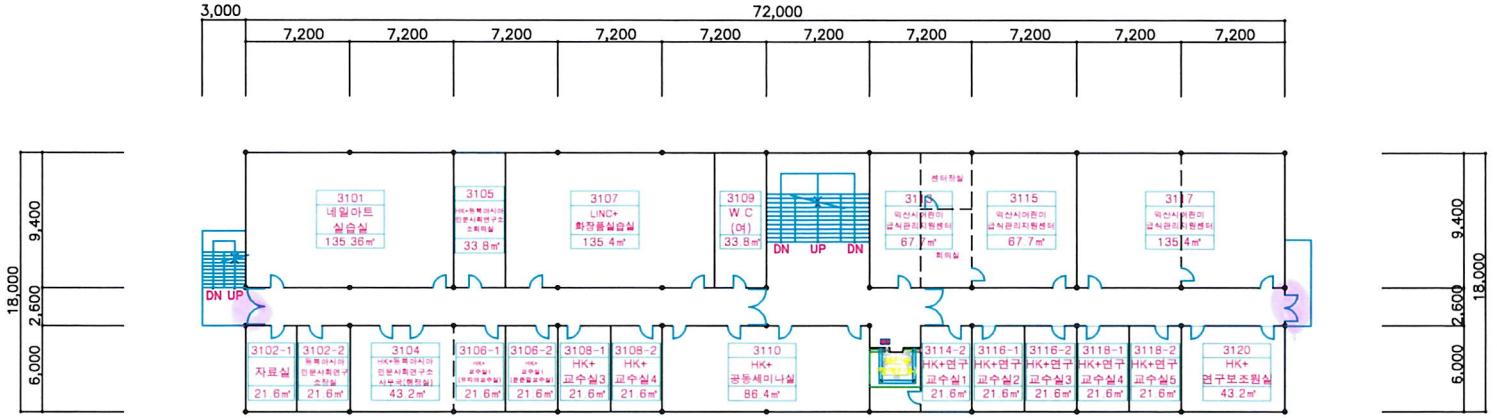

3층평면도

?????
WONKWANG UNIVERSITY

※ NOTE

실번호	0000-0
실명	0 0 0
면적	000㎡

수정날짜 : 2023. 03. 15


건 물 명

생 활 대


도 면 명

3층평면도
4층평면도

축 척	도면번호
NONE	96

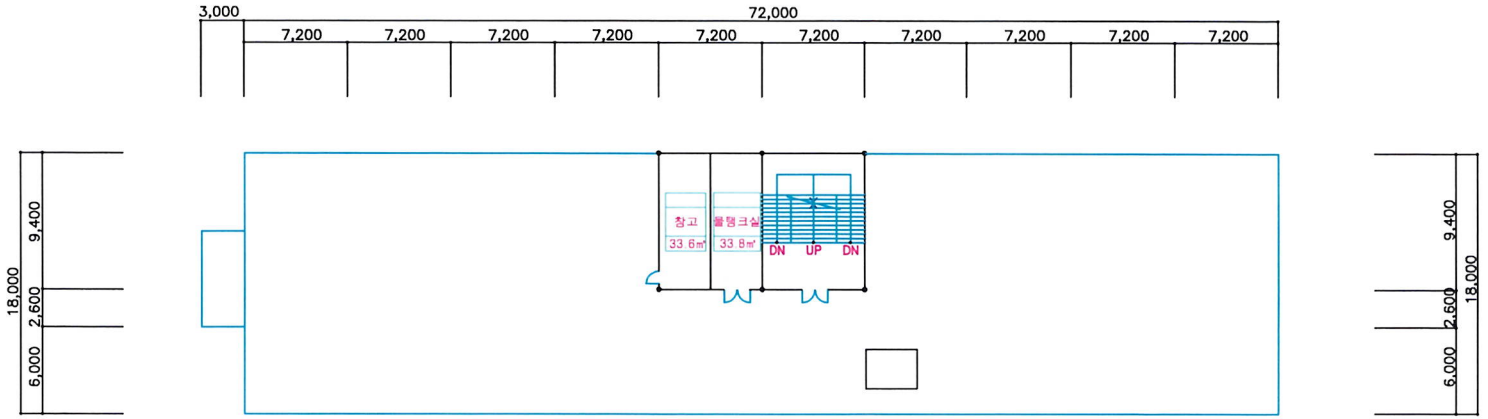

옥상평면도 S : 1/150

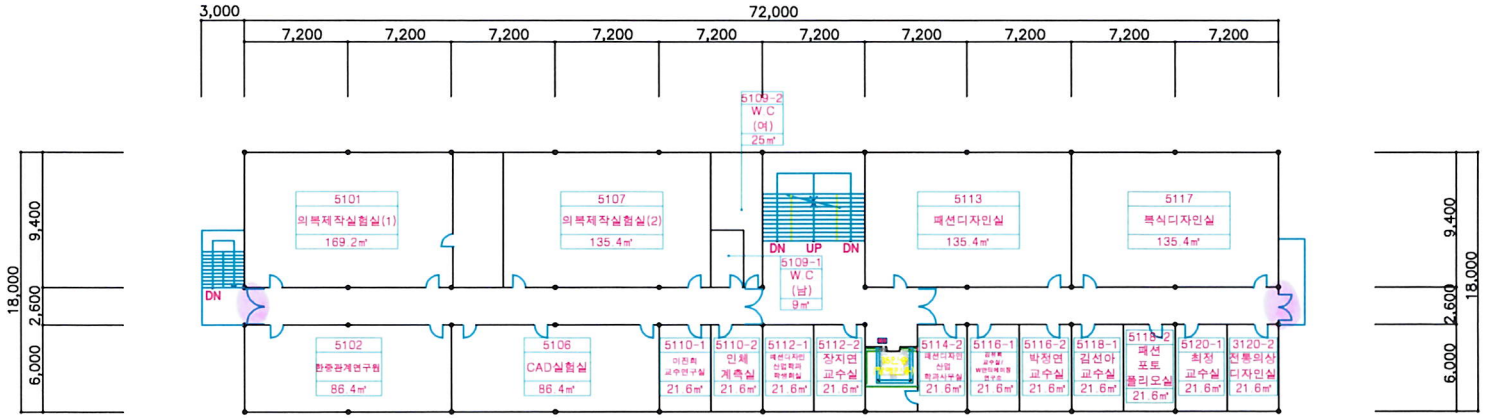

5층평면도 S : 1/150

WONKWANG UNIVERSITY

※ NOTE

실번호	0000-0
실명	0 0 0
면적	000㎡

수정날짜 : 2024. 02. 19

건 물 명

생 활 대

도 면 명

5층평면도
옥상층평면도

축 척	도면번호
NONE	97