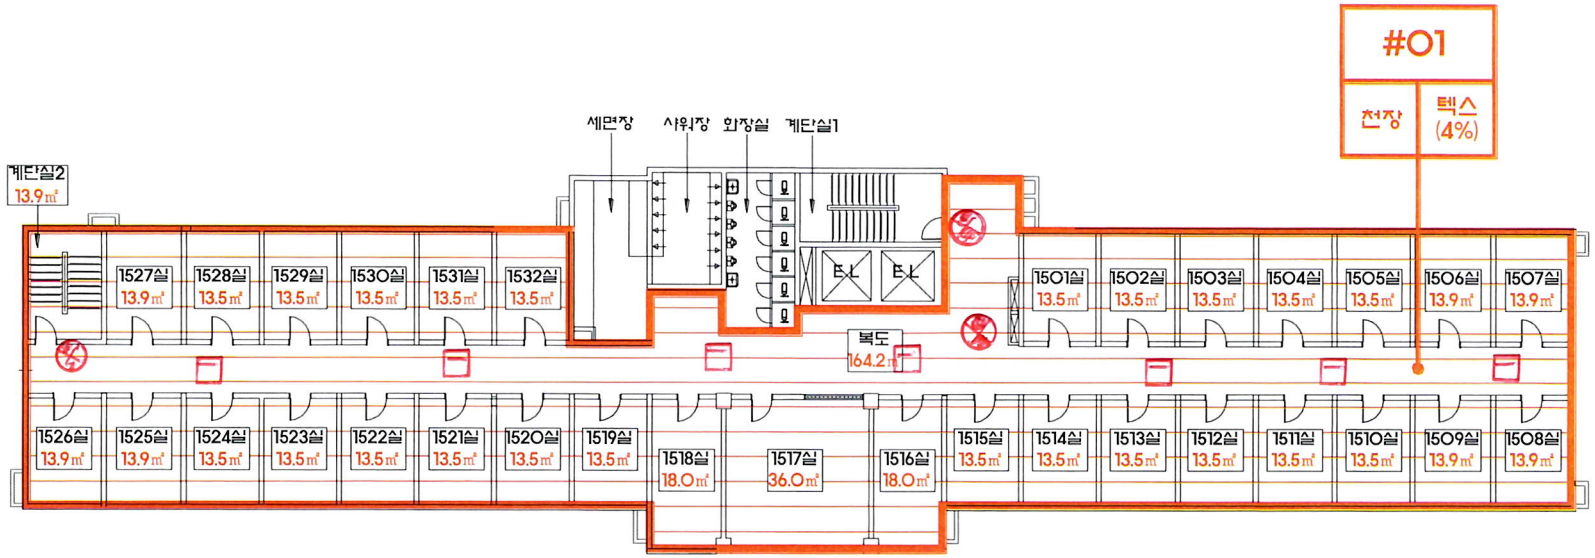


학림관 지상15층 석면지도

학림관 11F~15F

텍스 3166.4㎡

<석면표시 범례>

그림	건축 자재명	그림	건축 자재명
	지붕재		천장재
	벽재		바닥재
	분무재 (뿜칠재)		내화 (피복재)
	배관재 (보온)		배관재 (연결)
	기타 물질		칸막이

<건축자재 인식표>


시료번호 (시료위치 / 건축자재) — 석면 비함유 시료

시료번호 (시료위치 / 건축자재 (함유율)) — 석면 함유 시료

<지도개요>

구분	실명	내용

건축물명
44. 학림관
도면번호
44-01
석면지도 수정기관
㈜대한환경기술원

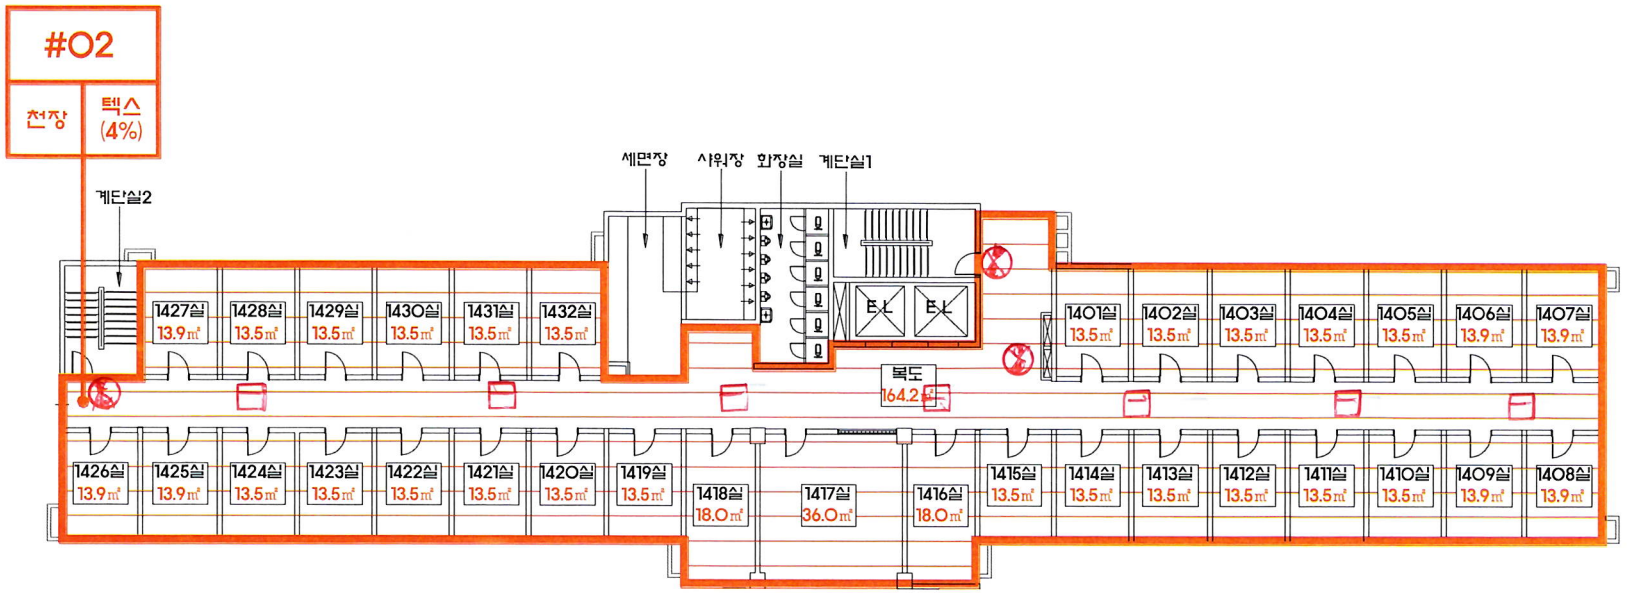

학림관 지상14층 석면지도

<석면표시 범례>

그림	건축 자재명	그림	건축 자재명
	지붕재		천장재
	벽재		바닥재
	분무재 (뿜칠재)		내화 (피복재)
	배관재 (보온)		배관재 (연결)
	기타 물질		칸막이

<건축자재 인식표>



석면 비함유 시료




석면 함유 시료

<지도개요>

구분	실명	내용

건축물명
44. 학림관
도면번호
44-02
석면지도 수정기관
㈜대한환경기술원

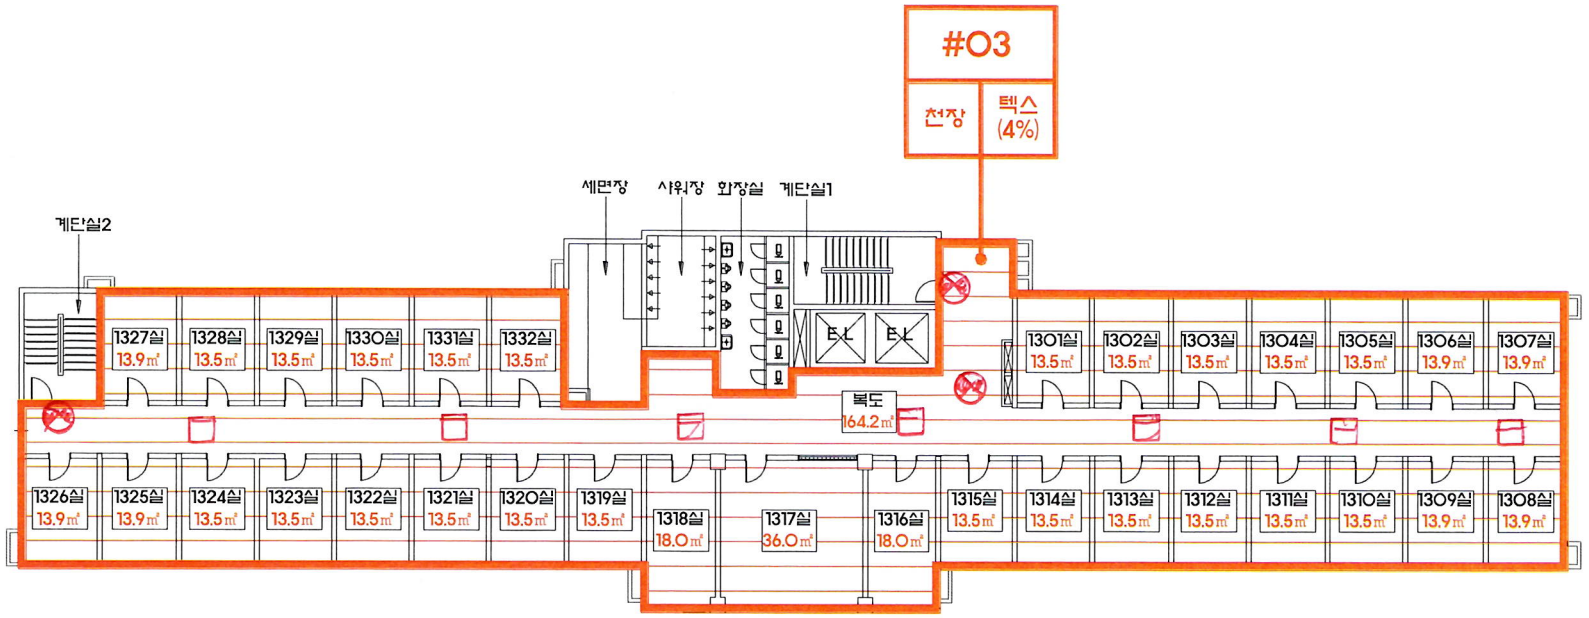

학림관 지상13층 석면지도

<석면표시 범례>

그림	건축 자재명	그림	건축 자재명
	지붕재		천장재
	벽재		바닥재
	분무재 (뿜칠재)		내화 (피복재)
	배관재 (보온)		배관재 (연결)
	기타 물질		칸막이


<건축자재 인식표>

시료번호		시료번호	
시료위치	건축자재	시료위치	건축자재 (함유율)
석면 비함유 시료		석면 함유 시료	

<지도개요>

구분	실명	내용

건축물명
44. 학림관
도면번호
44-03
석면지도 수정기관
㈜대한환경기술원

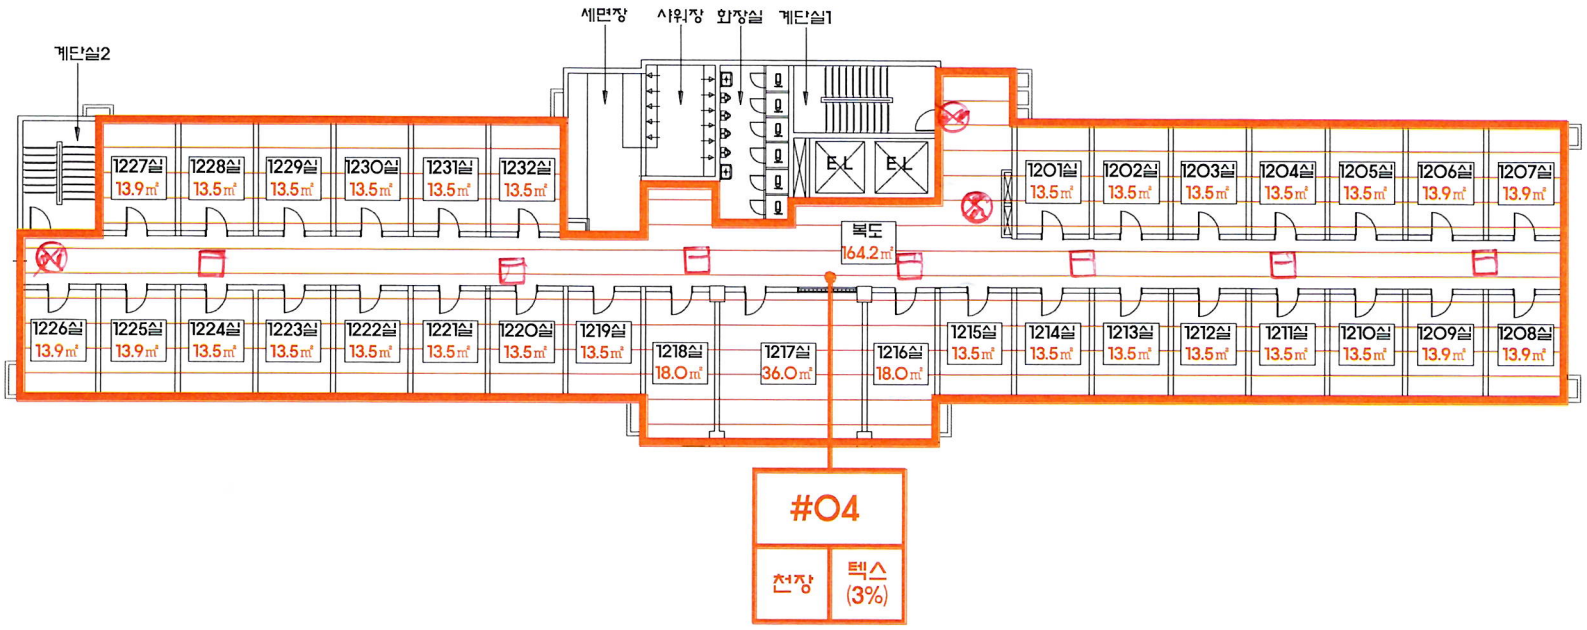

학림관 지상12층 석면지도

<석면표시 범례>

그림	건축 자재명	그림	건축 자재명
	지붕재		천장재
	벽재		바닥재
	분무재 (뿜칠재)		내화 (피복재)
	배관재 (보온)		배관재 (연결)
	기타 물질		칸막이


<건축자재 인식표>

시료번호		시료번호	
시료위치	건축자재	시료위치	건축자재 (함유율)
석면 비함유 시료		석면 함유 시료	

<지도개요>

구분	실명	내용

건축물명
44. 학림관
도면번호
44-04
석면지도 수정기관
㈜대한환경기술원

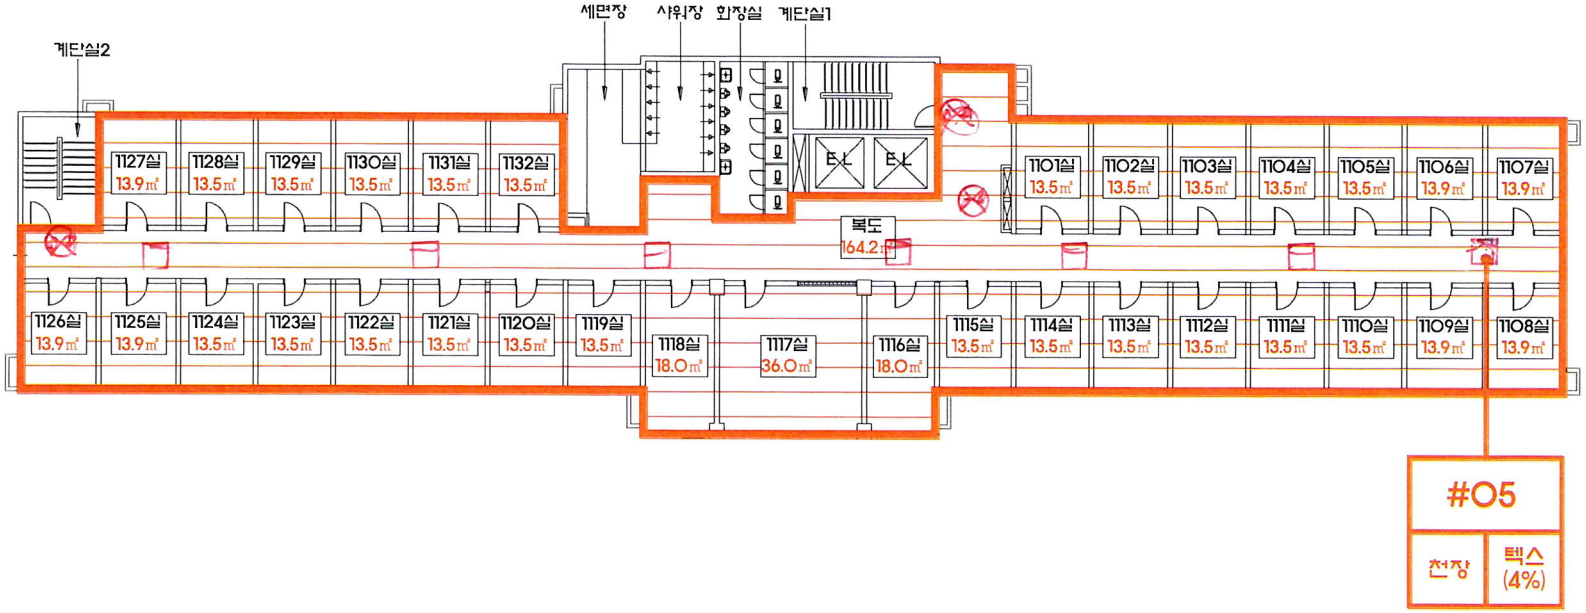

학림관 지상11층 석면지도

구분	실명	내용

<석면표시 범례>

그림	건축 자재명	그림	건축 자재명
	지붕재		천장재
	벽재		바닥재
	분무재 (뿜칠재)		내화 (피복재)
	배관재 (보온)		배관재 (연결)
	기타 물질		칸막이

<건축자재 인식표>



<지도개요>

건축물명
44. 학림관
도면번호
44-05
석면지도 수정기관
㈜대한환경기술원