




WONKWANG UNIVERSITY

※ NOTE

실번호	0000-0
실명	0 0 0
면적	000㎡

NOTE

1. 실외기는 지상에 설치할 것.
2. 배관 노출부위 스탠카바 작업할 것.
3. 드레인인 PVC 작업할 것.
4. 방화품, 방화실리콘 마감할 것.
5. FI-BOX는 각 실내에 설치 예정.
6. 각 실외기에 호실번호 기재.
7. 실외기는 일자발 설치할것.

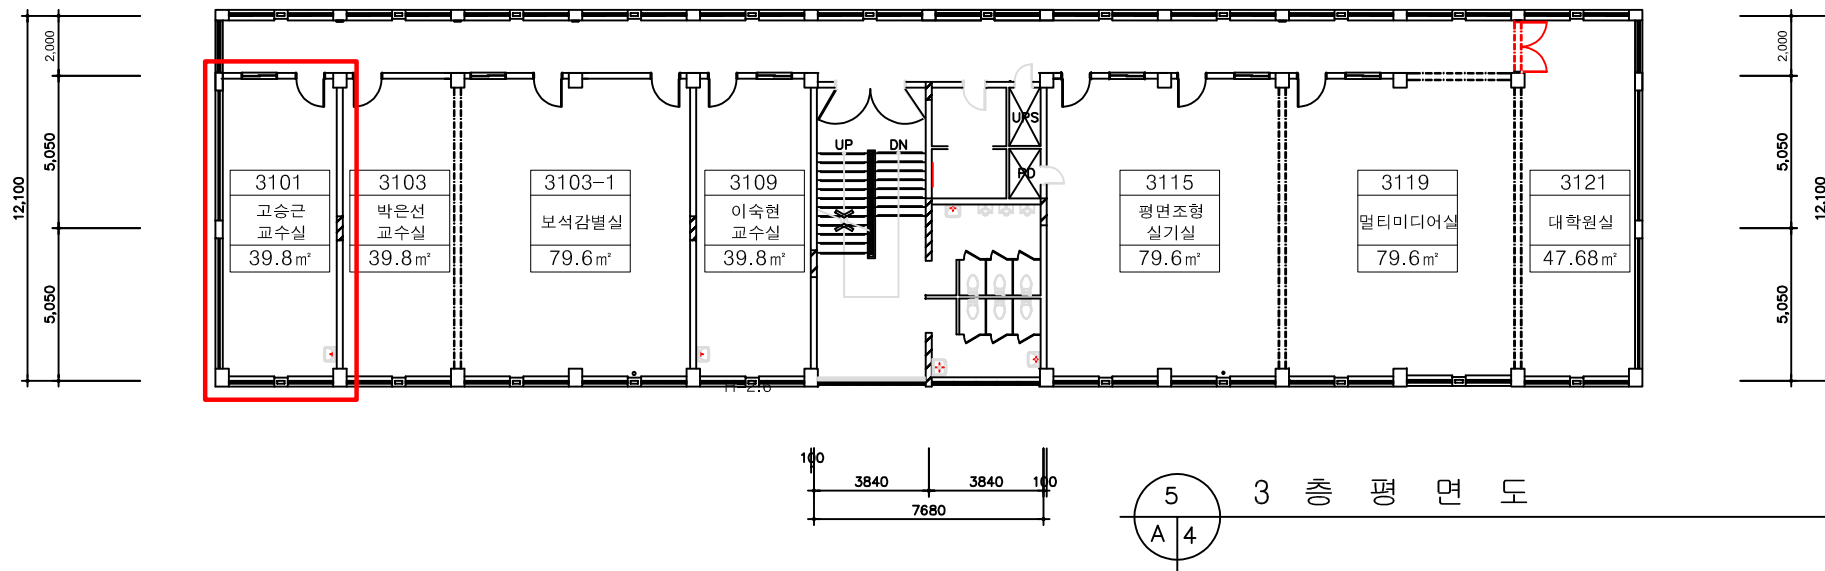

수정날짜 : 2020. 03. 11

건 물 명

도예관

도 면 명

3층 및 옥탑
옥상 평면도

축 작

도 면 번호


41



원광대학교
WONKWANG UNIVERSITY

※ NOTE

실번호	0000-0
실명	0 0 0
면적	000㎡

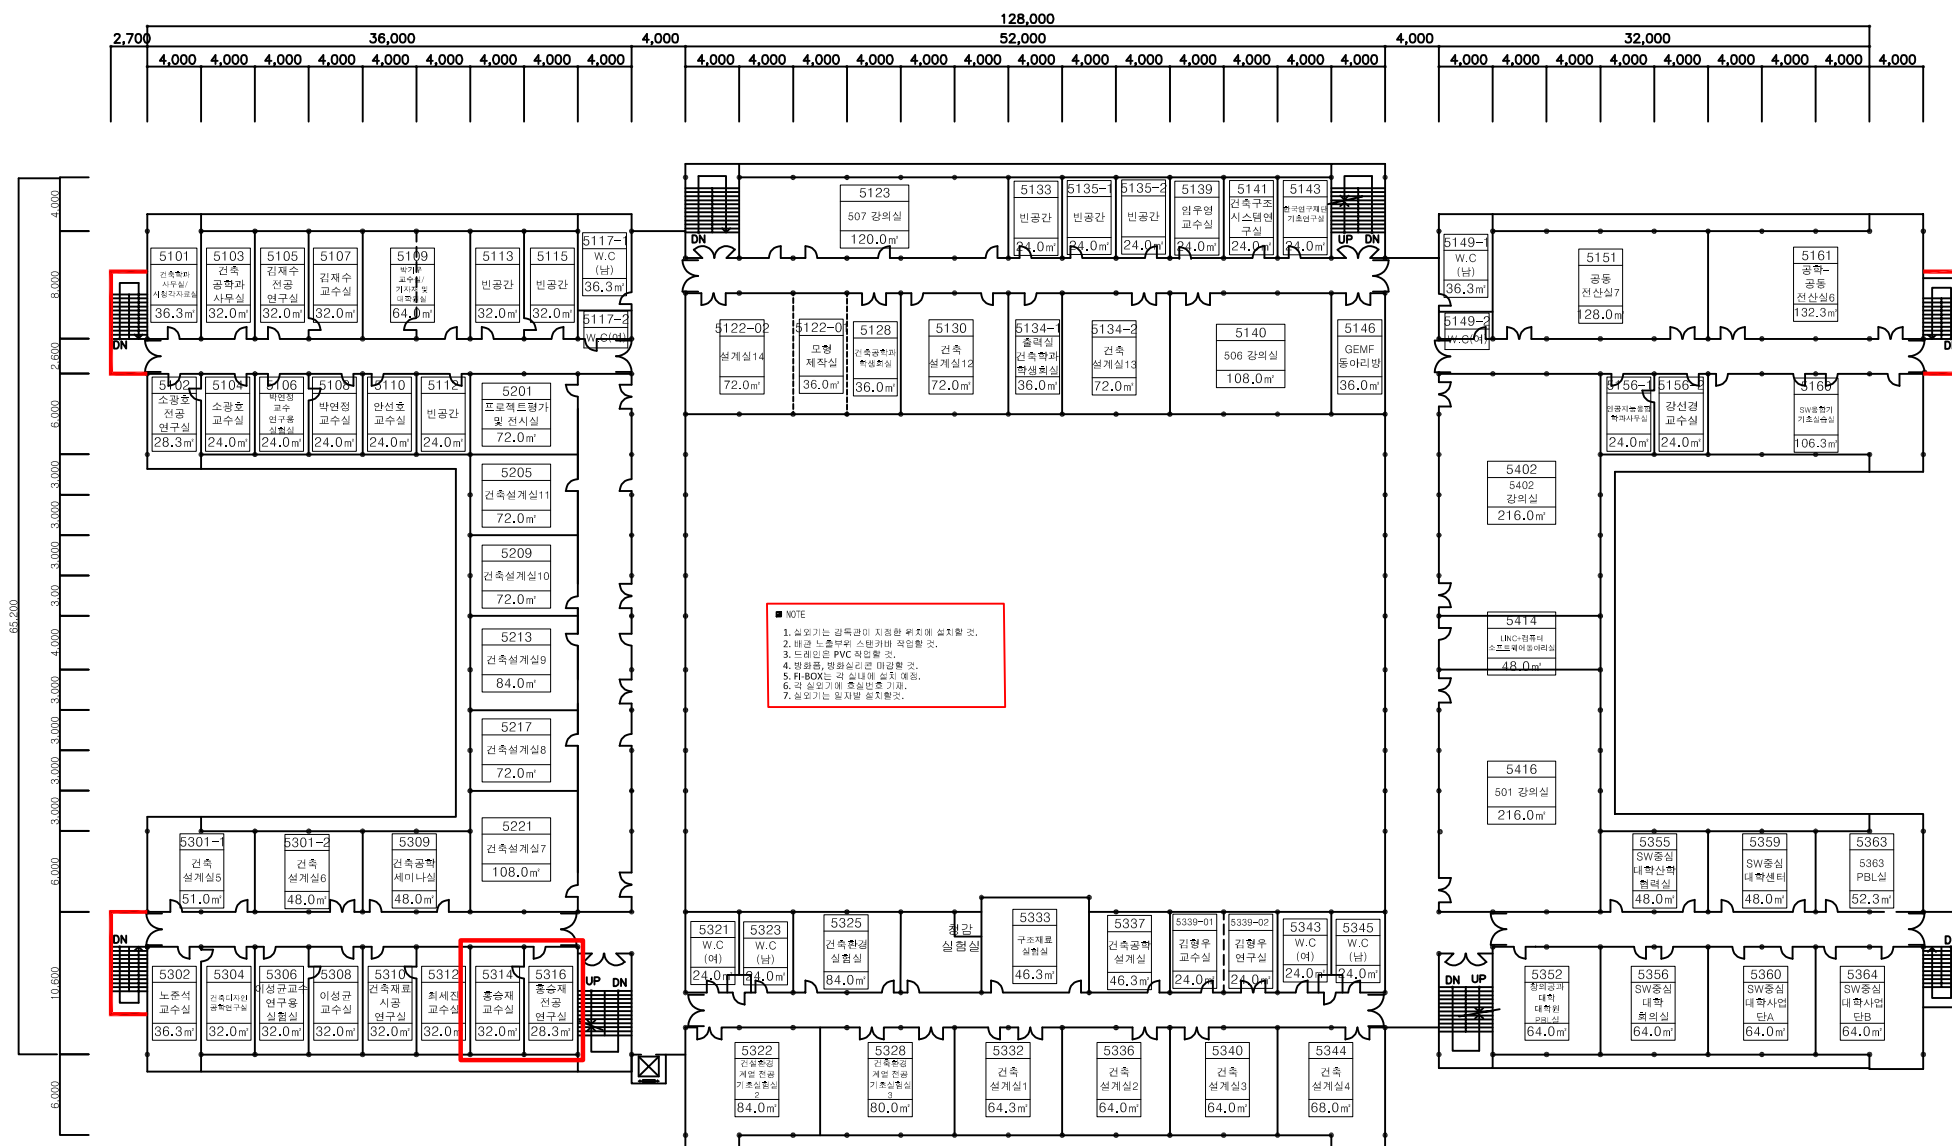

5층 평면도 S : NONE

수정날짜 : 2022. 06. 08

건물명	공학관
도면명	5층 평면도
축척	none
도면번호	22




WONKWANG UNIVERSITY

NOTE

1. 실외기는 지상에 설치할 것.
2. 드레인인 PVC 작업할 것.
3. 방화폼, 방화실리콘 마감할 것.
4. FI-BOX는 각 실내에 설치 예정.
5. 각 실외기에 호실번호 기재.
6. 실외기는 일자발 설치할 것.

2층평면도

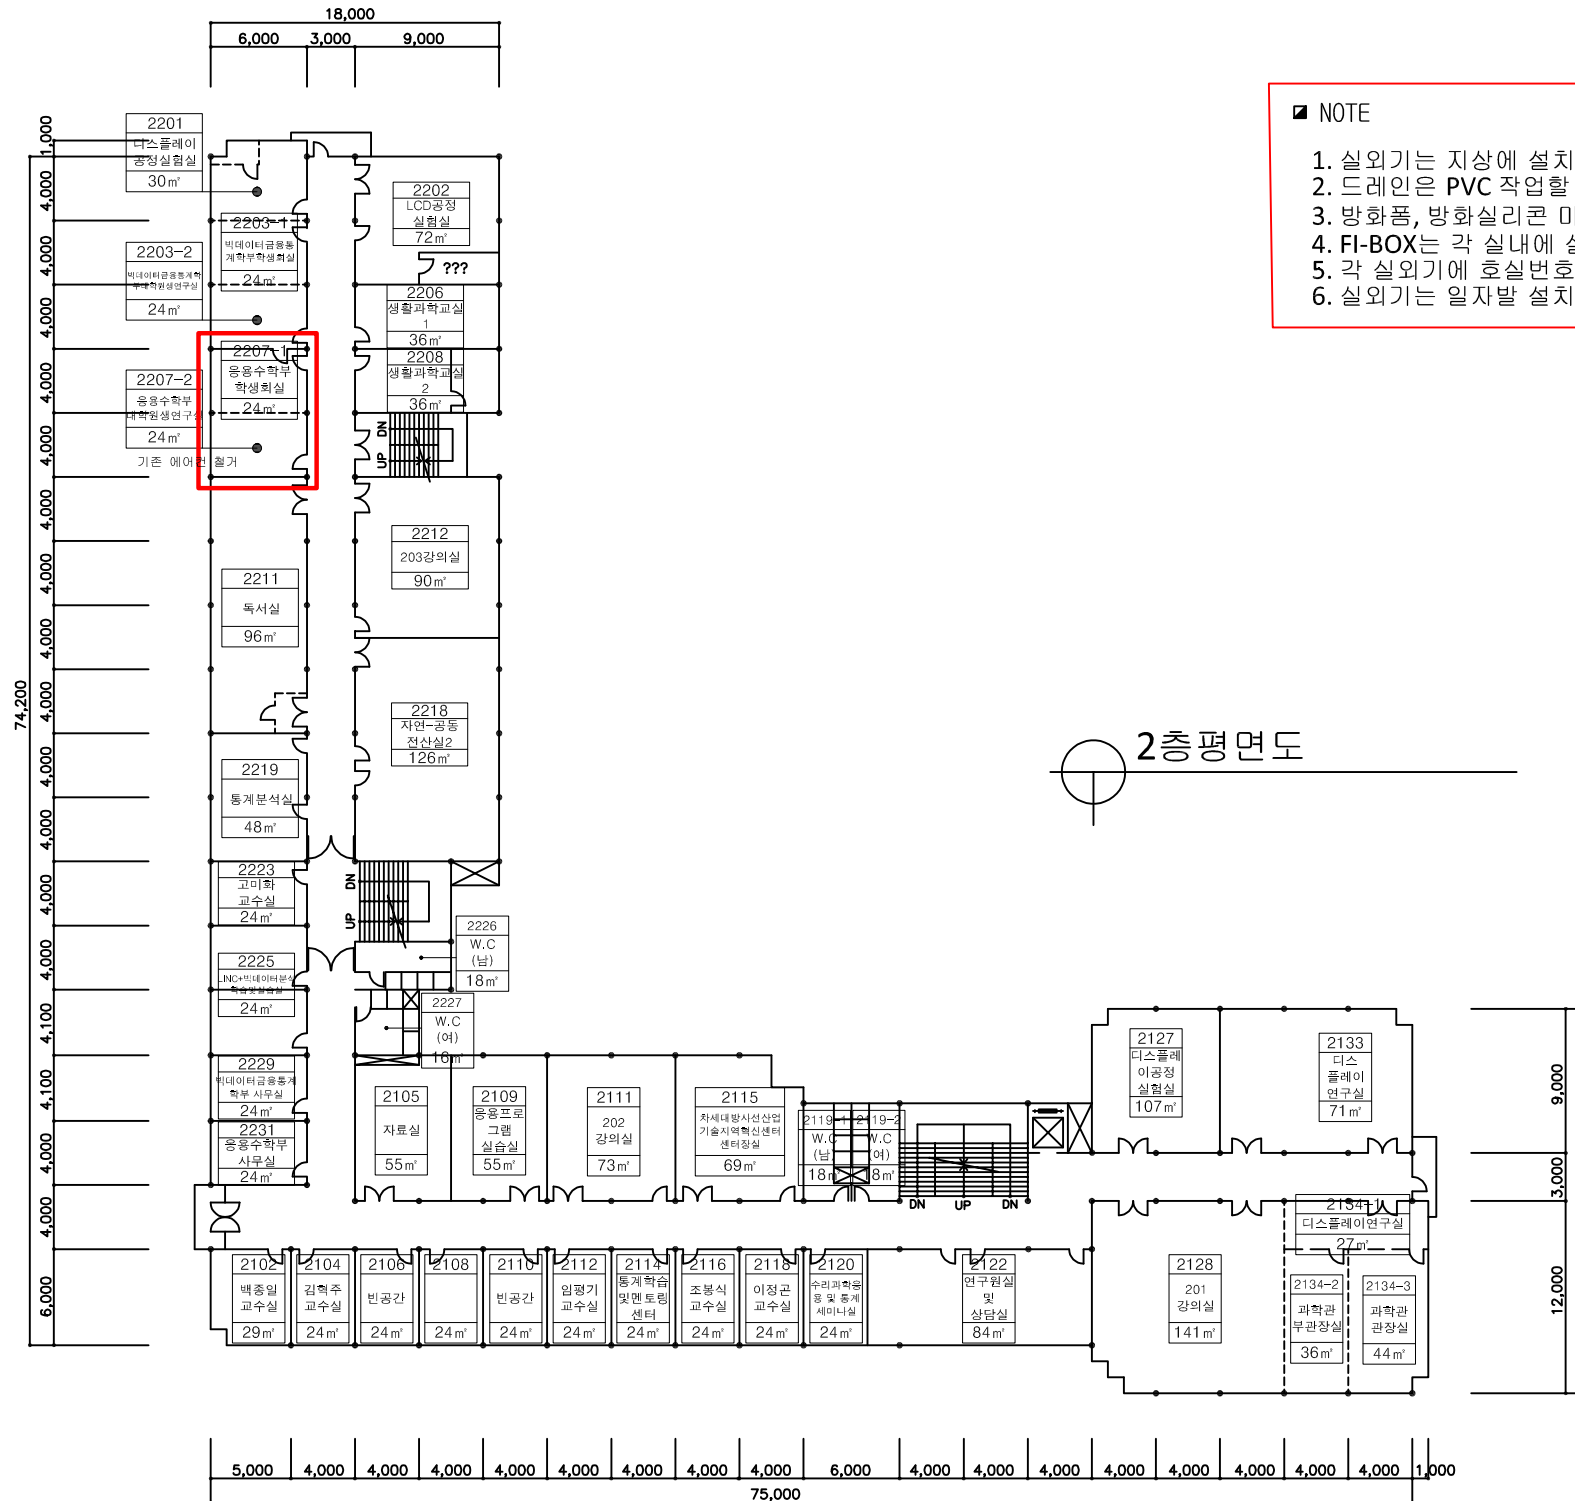

수정날짜 : 2022. 03. 10

건물명

자연과학관

도면명

2층평면도

속칙

NONE

도면번호

135




WONKWANG UNIVERSITY

NOTE

1. 실외기는 지상에 설치할 것.
2. 드레인은 PVC 작업할 것.
3. 방화폼, 방화실리콘 마감할 것.
4. FI-BOX는 각 실내에 설치 예정.
5. 각 실외기에 호실번호 기재.
6. 실외기는 일자발 설치할 것.

3층평면도

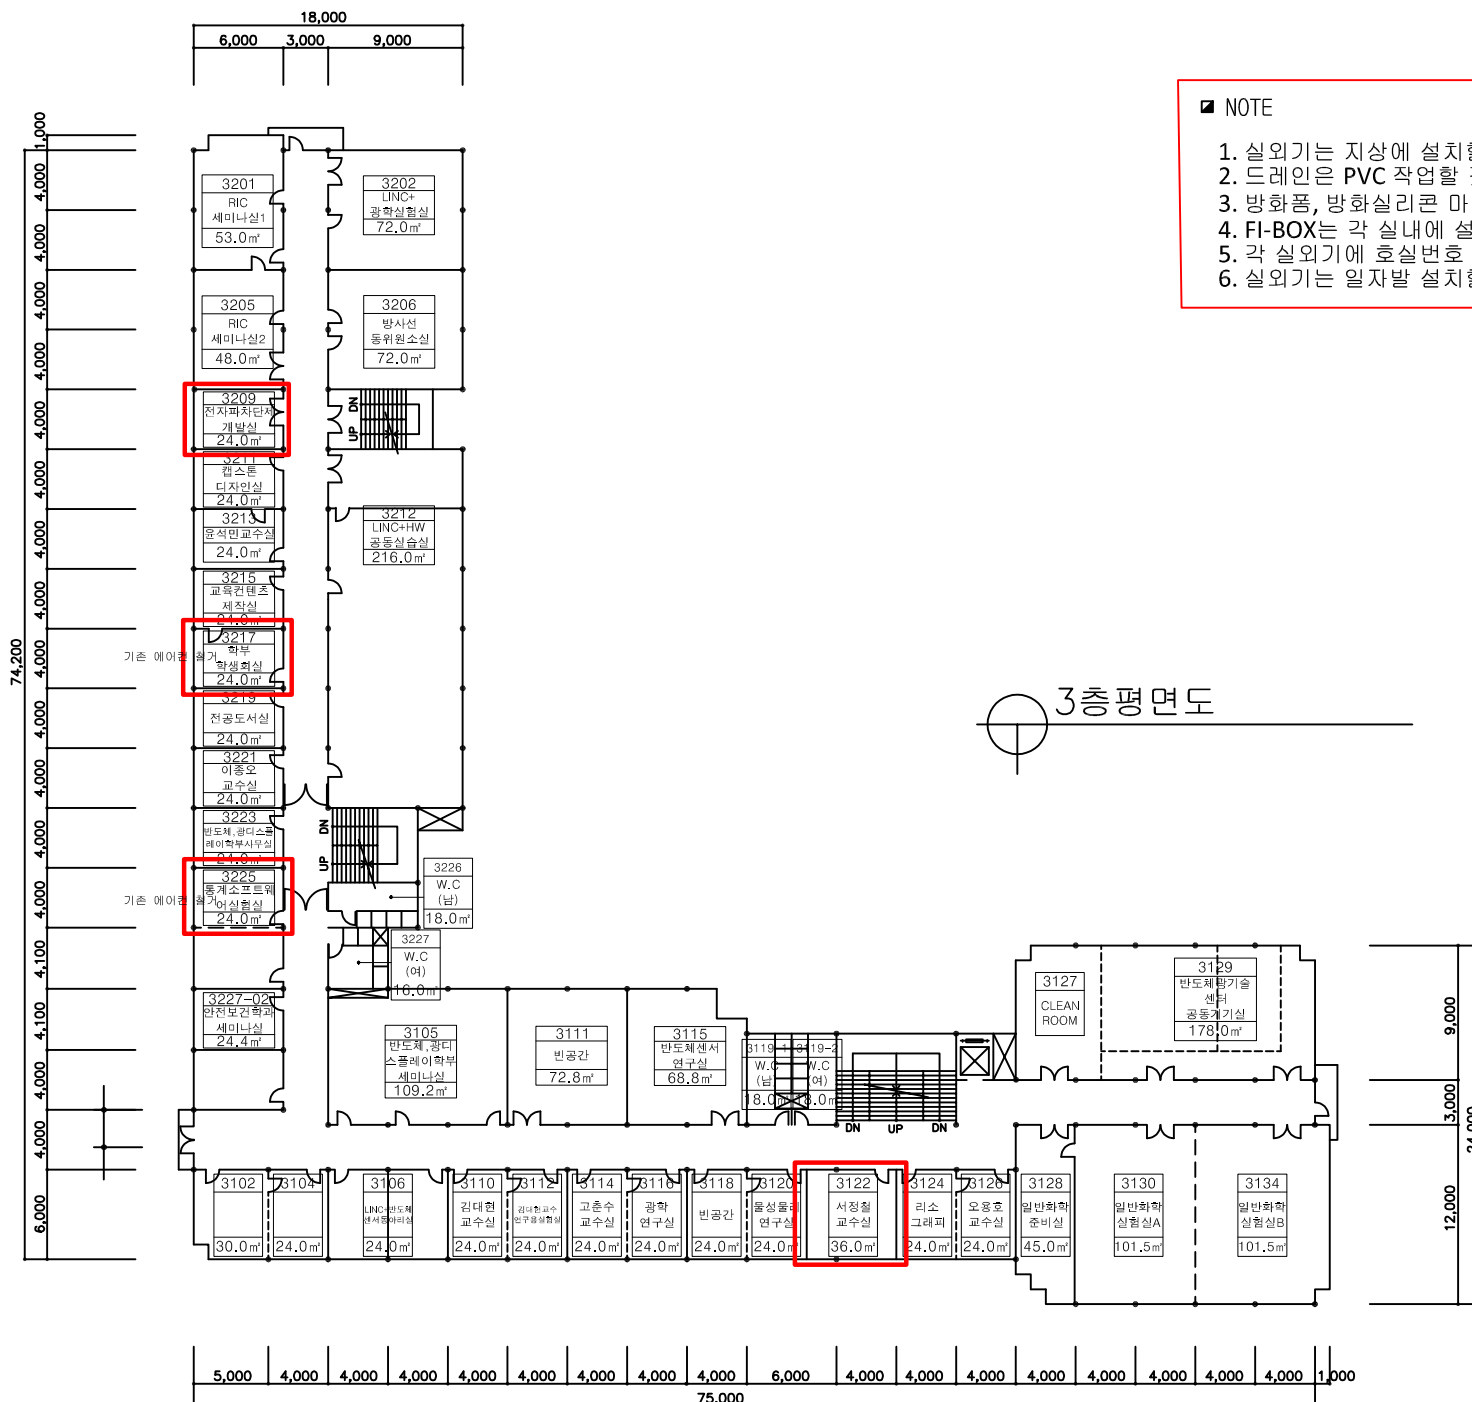

수정날짜 : 2022. 06. 08

건물명

자연과학관

도면명

3층평면도

출처

NONE

도면번호

136