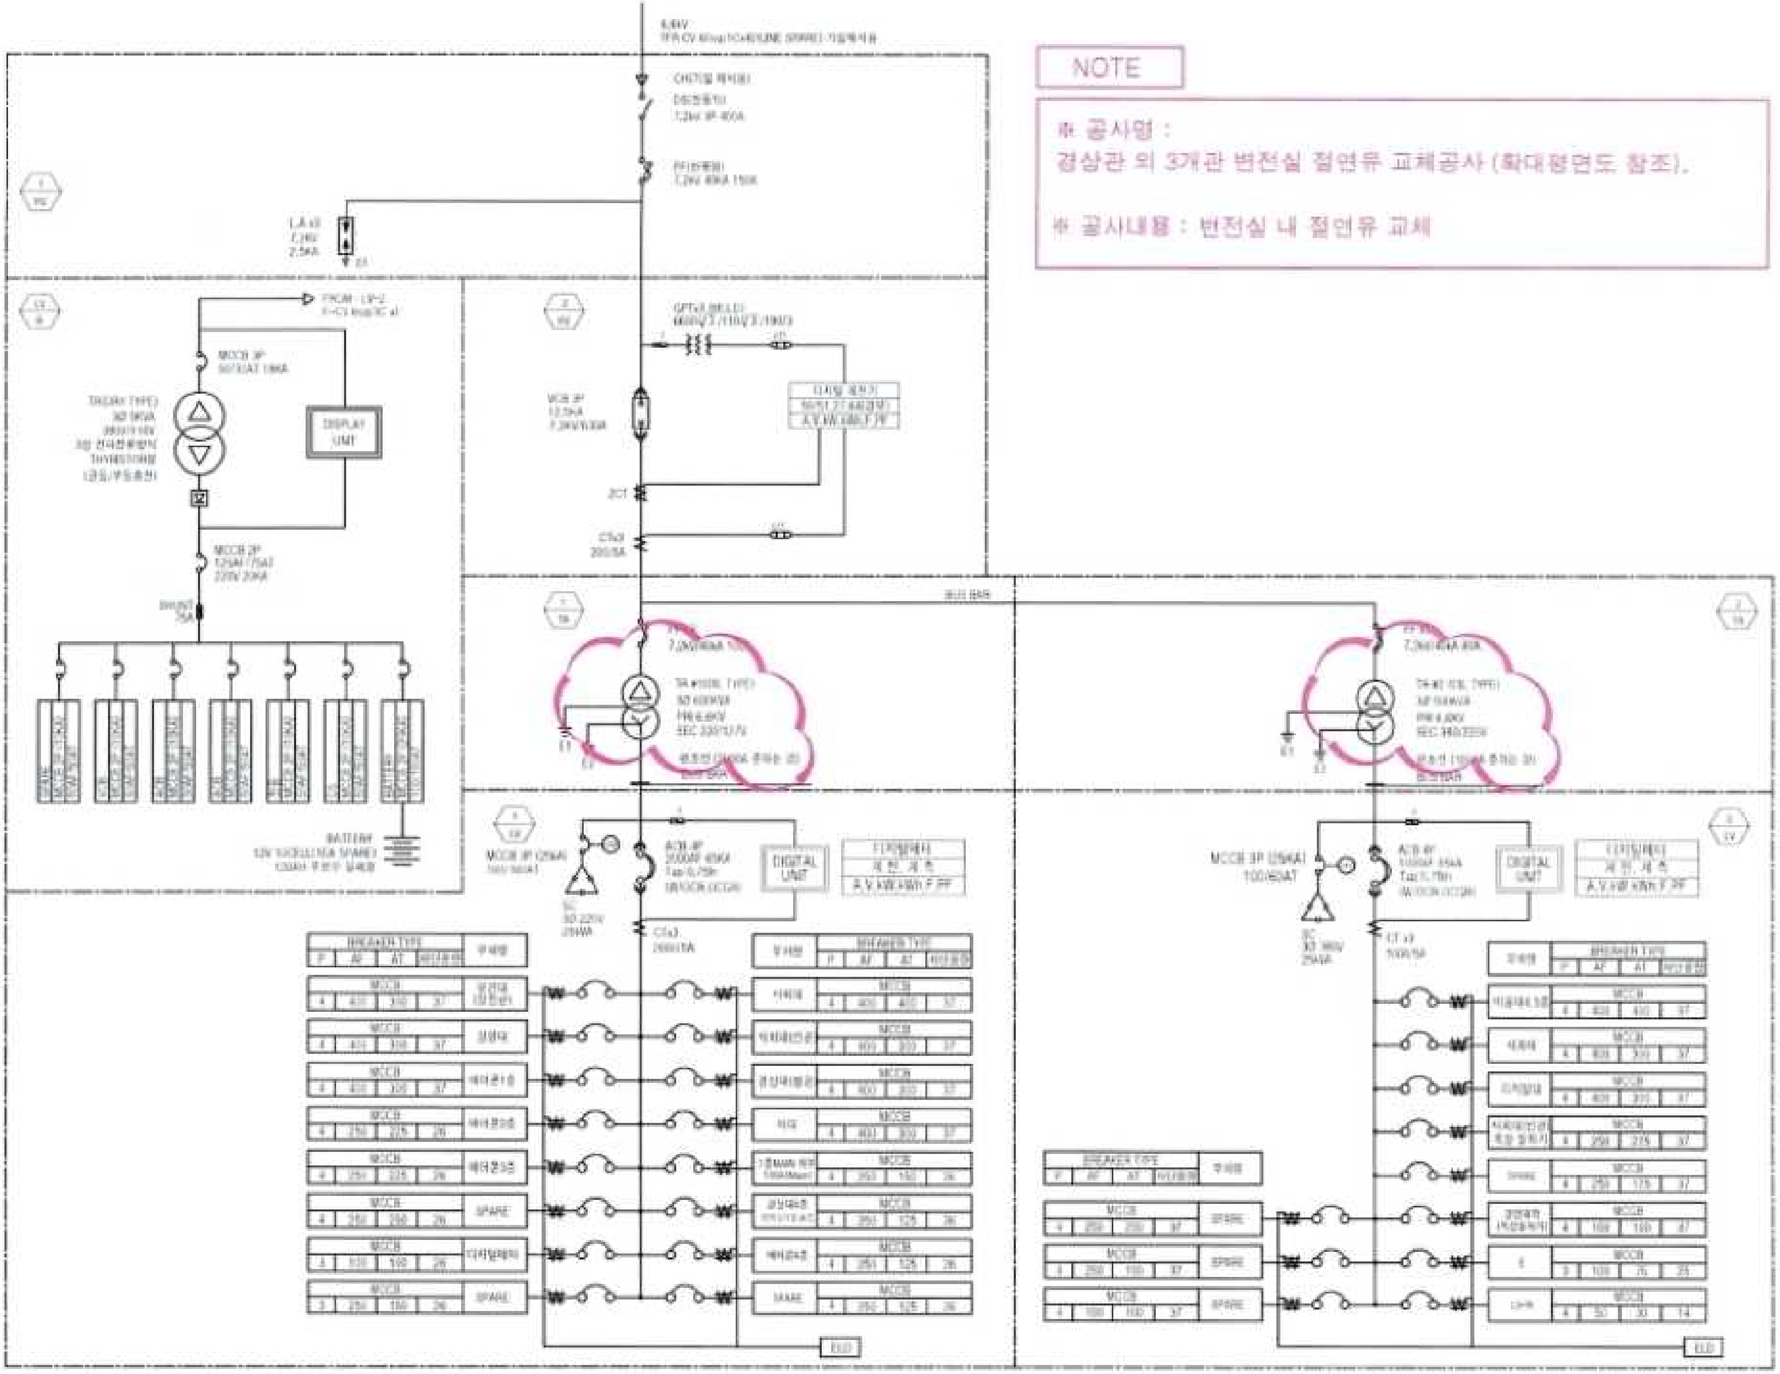

NOTE

※ 공사명 :
경상관 외 3개관 변전실 절연유 교체공사 (확대평면도 참조).

※ 공사내용 : 변전실 내 절연유 교체

* 최대전력제어장치용 CT, 네트워크장치, 계측관 재설치는 감독관 또는 감리자와 협의후 시공할 것

[경영대]
수변전설비 단선결선도

SCALE : 1/NONE(A3)

원광대학교
WONKWANG UNIVERSITY
원광대학교

[경영대]
수변전설비 단선결선도

E - 003

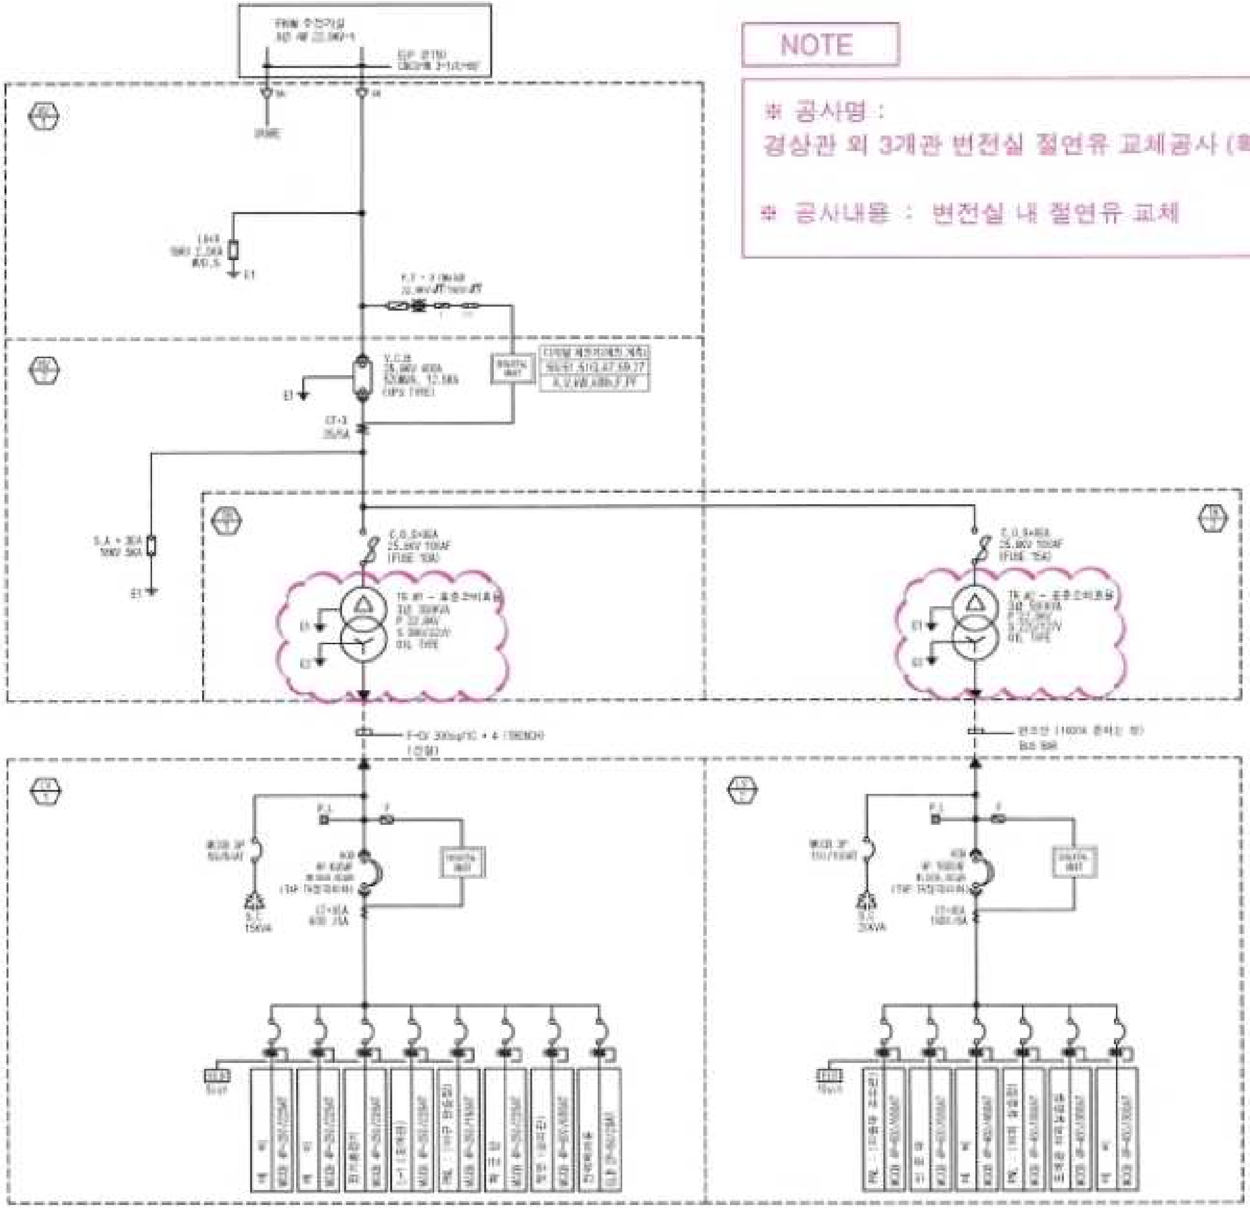

• 모든 차단기는 30KA 이상 적용

NOTE

※ 공사명 :
경상관 외 3개관 변전실 절연유 교체공사 (확대평면도 참조).

※ 공사내용 : 변전실 내 절연유 교체

[조소관]

수변전설비 단선결선도

SCALE : 1/NONE (A3)

원광대학교

생명자원관, 조소관
변전실 교체공사

E - 003

NOTE

※ 공사명 :
경상관 외 3개관 변전실 절연유 교체공사 (확대평면도 참조).

※ 공사내용 : 변전실 내 절연유 교체

- 용량증설 : 기존 400 KW + 5KW = 405KW
변경 400 KW + 300KW = 700KW

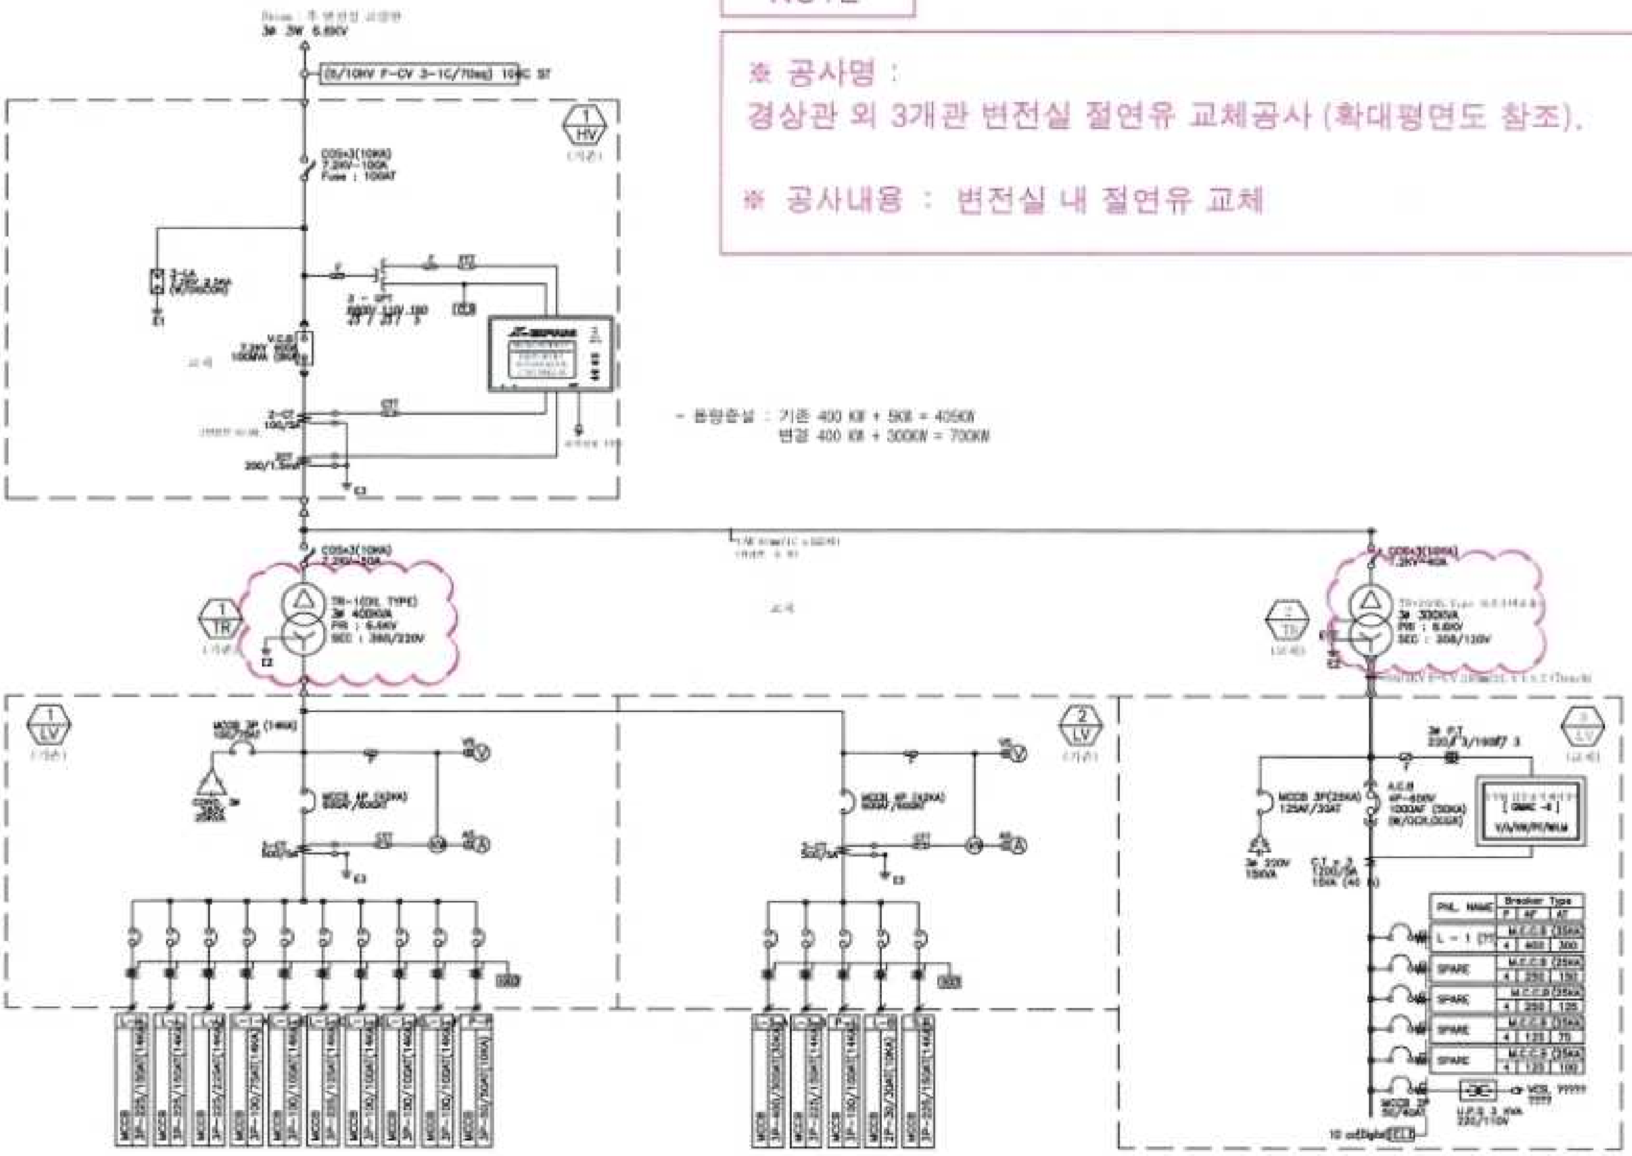

문화체육관 지하 6.6KV수전설비 결선도

SCALE 1/N.S(A1), 1/N.S(A3)

PROJECT TITLE
NOTE
NO.
DATE
DESIGNED BY
DRAWN BY
CHECKED BY
APPROVED BY
NAME OF DRAWING
SCALE
A1 : 1 / N.S
A3 : 1 / N.S
DATE
2019. 09
DRAWING NO.
E - 0 6
SHEET NO.

변경후

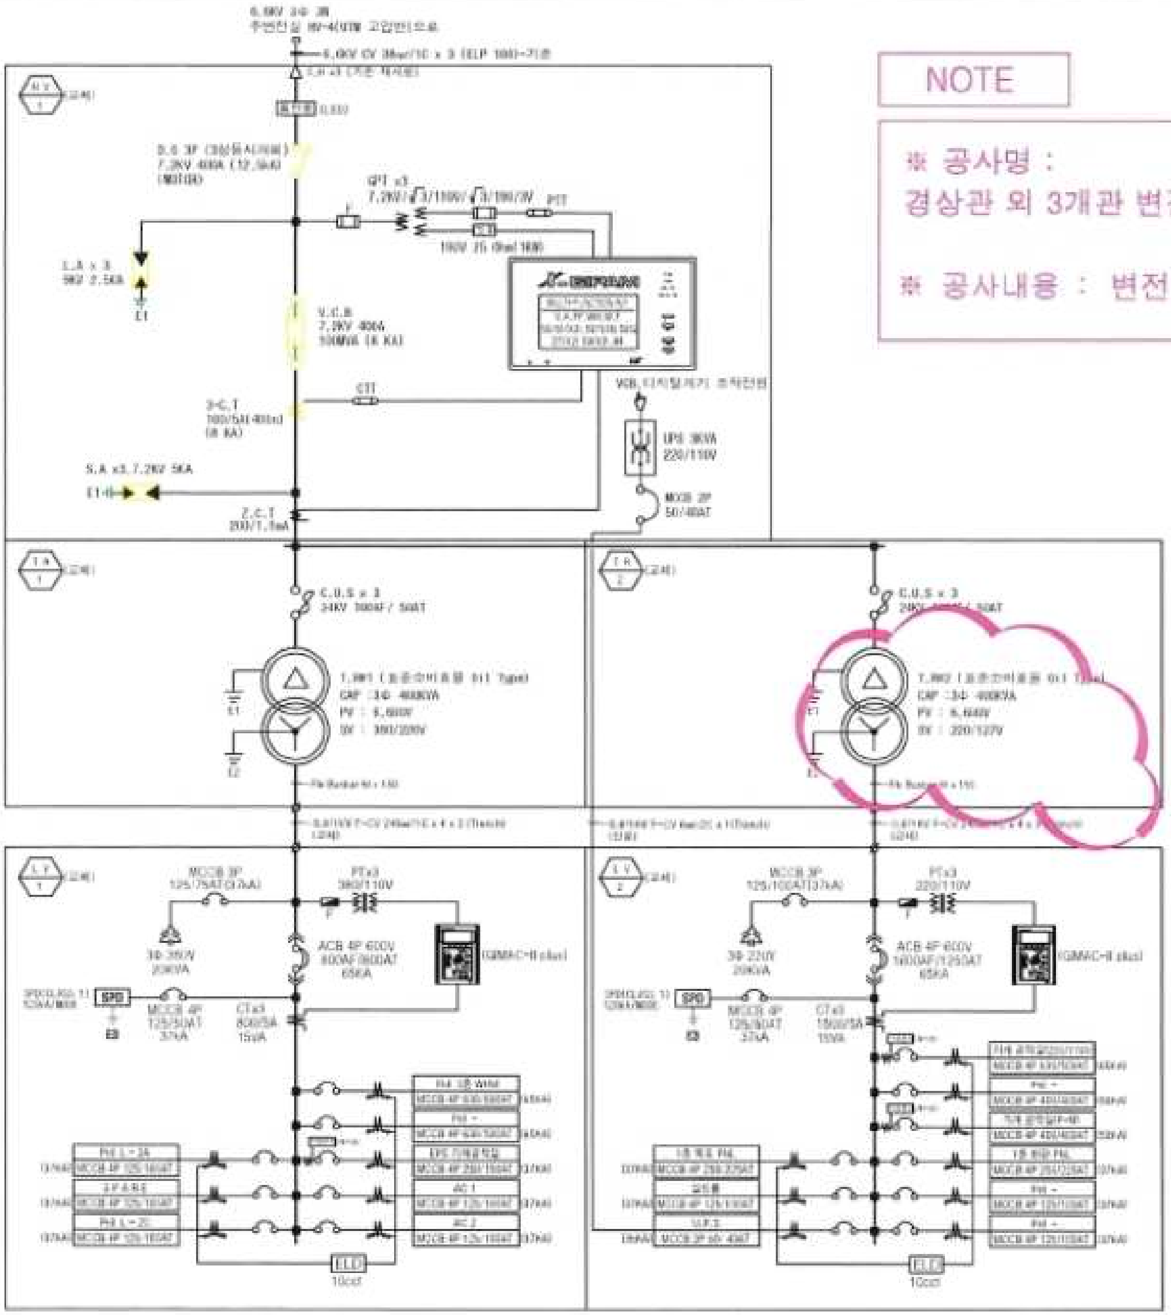

NOTE

※ 공사명 :
경상관 외 3개관 변전실 절연유 교체공사 (확대평면도 참조).

※ 공사내용 : 변전실 내 절연유 교체

공학교육혁신관 6.6KV 수변전 단선결선도

SCALE : 1/N,S (A1), 1/N,S (A3)

공 사 명	시 행 청	용 역 회 사	축 척	설계일자				도 면 명	도면번호
자연과학관 외 3개소 변전실 교체공사	원 광 대 학 교	대한엔지니어링	1 : N.S (A3)	2024. 07	[illegible]			공학교육혁신관 변전실 6.6KV수변전 단선결선도(변경후)	E - 09